


North Gatehouse Building

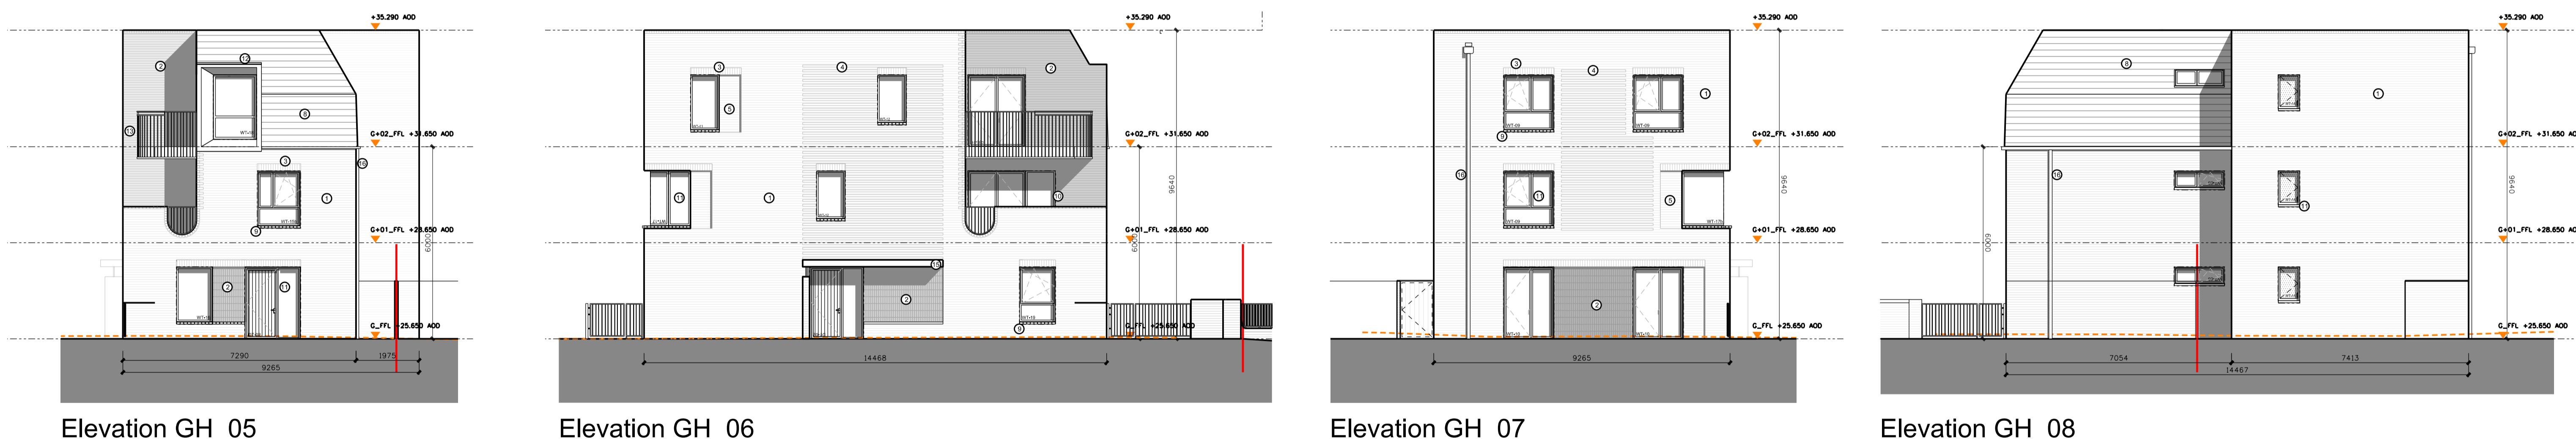

South Gatehouse Building


\* Landscaping omitted for clarity

#### Gatehouse buildings elevations

Revision	Date	Description	By	Check	Client logo
<b>Draft planning issue 30/06/21</b>					

Notes  
Do not scale drawings. All dimensions should be checked on site. Errors to be reported to architect. To be read in conjunction with all relevant architects services drawings.  
Contractors, sub-contractors and suppliers must verify any critical dimensions on site prior to fabrication of any building element. Any discrepancies are to be reported to the architect.  
This drawing should be read in conjunction with all relevant specifications, engineers and specialists consultants information. Any discrepancies must be reported prior to installation.

Key  
1. Main brick: Reddish/brown brick with light mortar  
2. Header bond brick  
3. Soldier course bond brick  
4. Protruding stretcher bond brick - 20mm  
5. Reindeer masonry - 100mm  
6. Sawtooth bond brickwork  
7. Brick arch lintel, header bond  
8. Clay pavers - light grey/red colour  
9. Brown glazed brick sill  
10. White composite window/door - RAL 2001 or similar  
11. Aluminium composite window/door - RAL 6013 or similar  
12. Dormer window surround - RAL 2001 or similar  
13. Balcony metal frame - RAL 2001 or similar  
14. Canopy PPC metal solid balustrade - RAL 2001 or similar  
15. Canopy PPC metal - RAL 2001 or similar  
16. Downwater pipe/piping - RAL 2001 or similar  
17. Privacy screen - RAL 2001 or similar

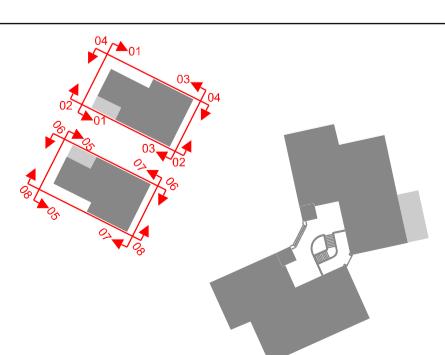


0 1m 5m 10m  
1:100 @ A1

**Metropolitan Workshop**


14-16 Cowcross Street  
London, EC1M 6DG  
+44 (0) 20 7566 0450  
www.metwork.co.uk

Project:	Farmstead Road
Client:	Phoenix Community Housing
Location:	Farmstead Road, Bellingham, London
Title:	Gatehouse Buildings Elevations
Date:	June 2021
Scale:	1:100 @ A1
Drawing Number:	1827
Job No.	P
Status	102
Package	100
Reference	00
Revision	

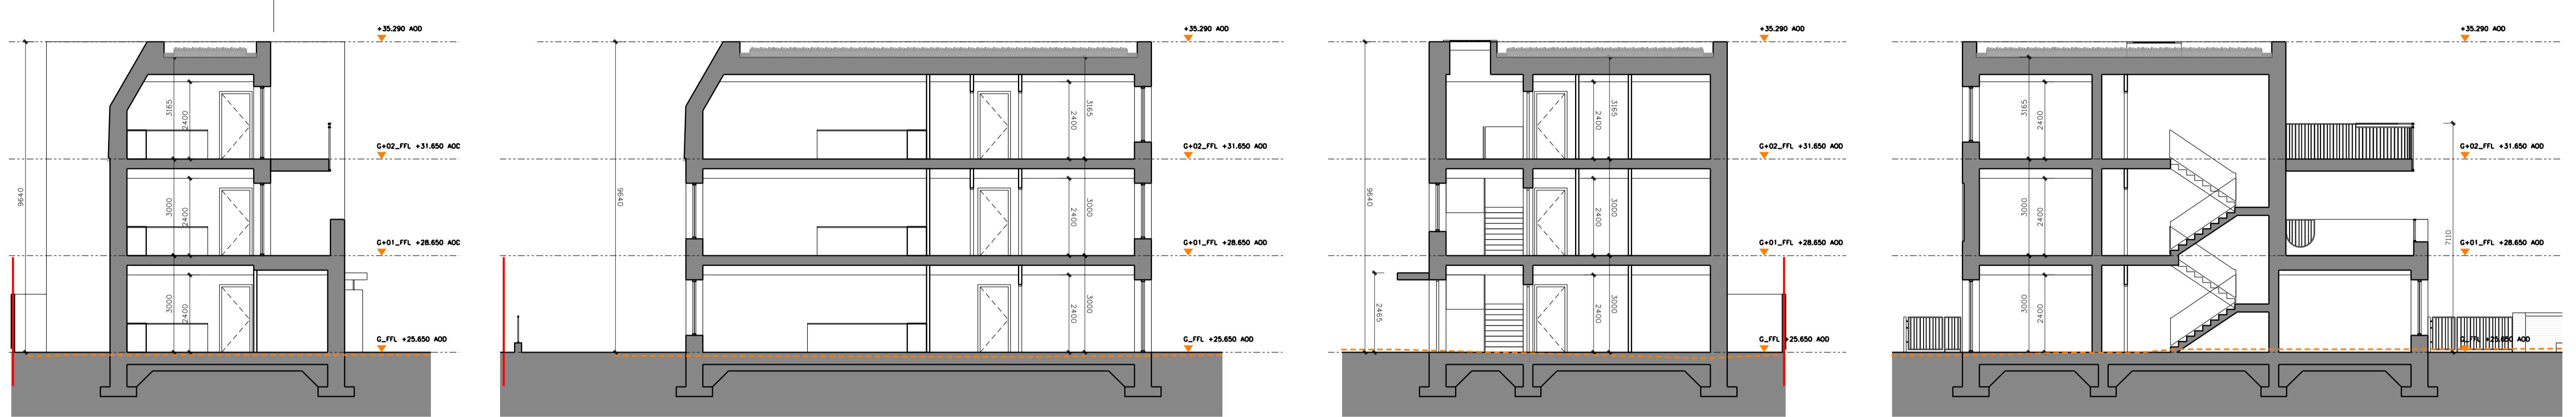

Section GH\_AA

North Gatehouse Building

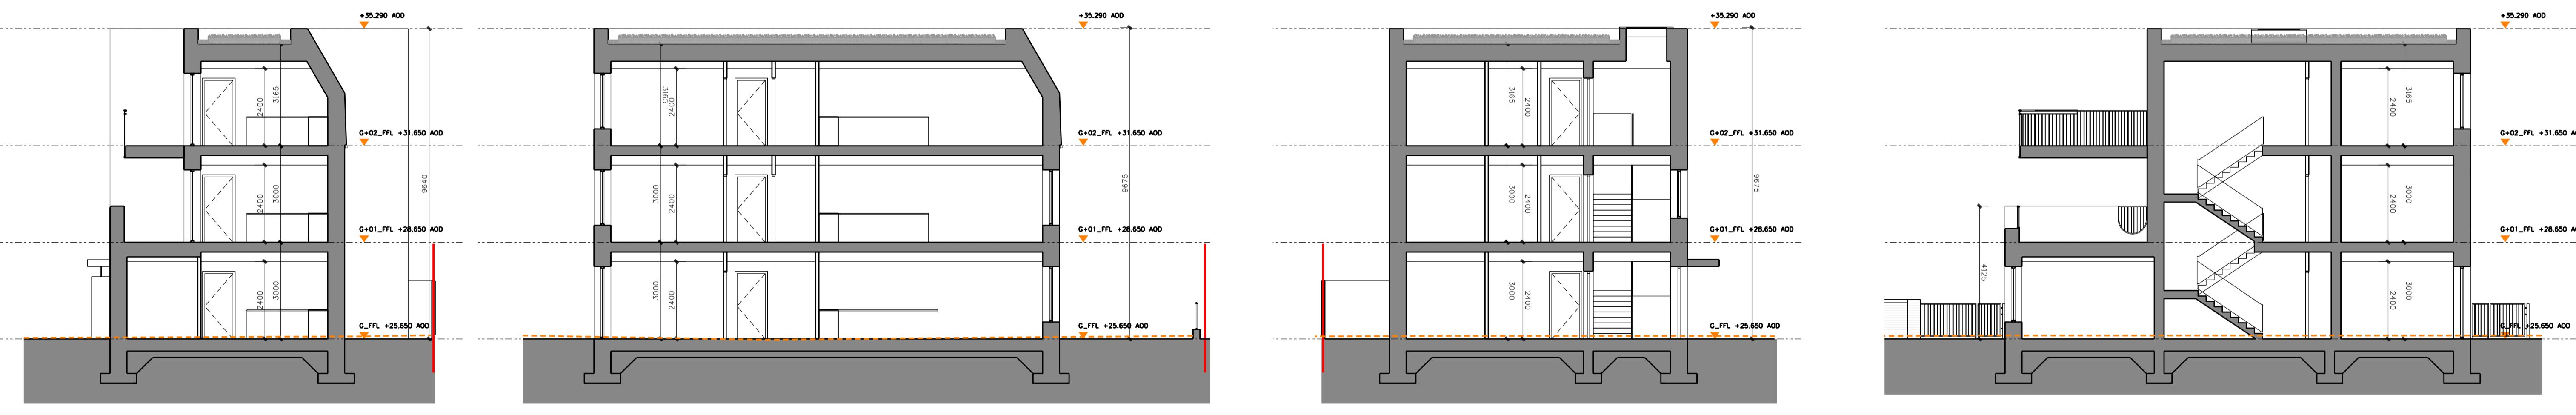


Section GH\_EE

South Gatehouse Building

\* Landscaping omitted for clarity


Gatehouse buildings sections

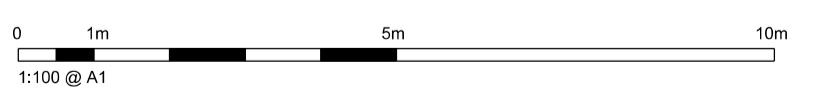

Revision	Date	Description	By	Check	Client logo
Draft planning issue	30/06/21	Phoenix Our community in our hands			

Notes  
Do not scale drawings. All dimensions should be checked on site. Errors to be reported to architect. To be read in conjunction with all relevant architects services drawings.  
Contractors, sub-contractors and suppliers must verify any critical dimensions on site prior to fabrication of any building element. Any discrepancies are to be reported to the architect.  
This drawing should be read in conjunction with all relevant specifications, engineers and specialists consultants information. Any discrepancies must be reported prior to installation.

Key

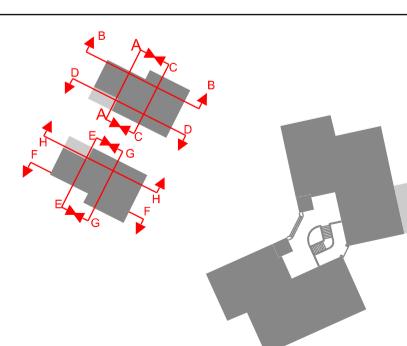

Metropolitan  
Workshop


14-16 Cowcross Street  
London, EC1M 6DG  
+44 (0) 20 7566 0450  
www.metwork.co.uk

Project:	Farmstead Road
Client:	Phoenix Community Housing
Location:	Farmstead Road, Bellingham, London
Title:	Gatehouse Buildings Sections
Date:	June 2021
Scale:	1:100 @ A1
Job No.:	1827
Status:	P
Package:	103
Reference:	100
Revision:	00


Drawing Number: 1827



Elevation BF\_01

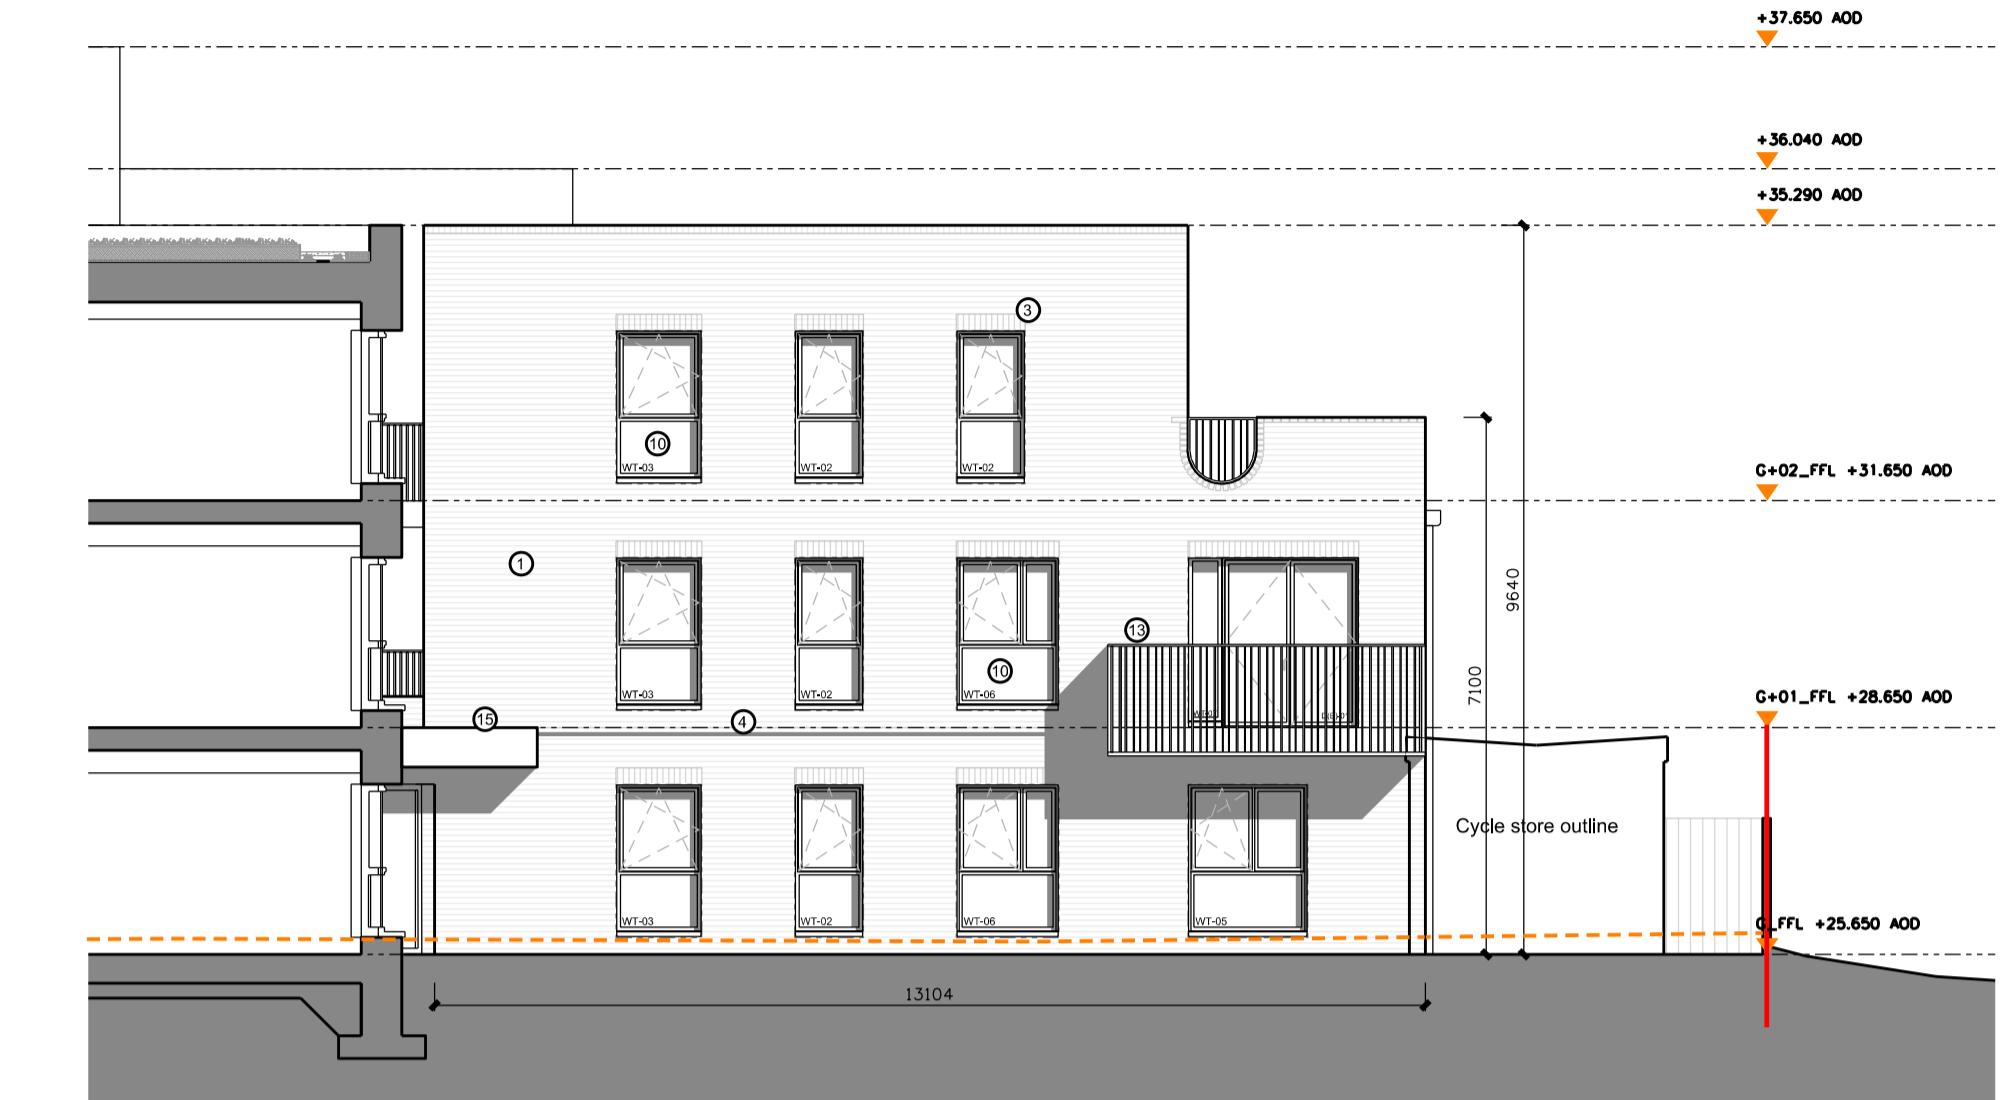

Elevation BF\_02

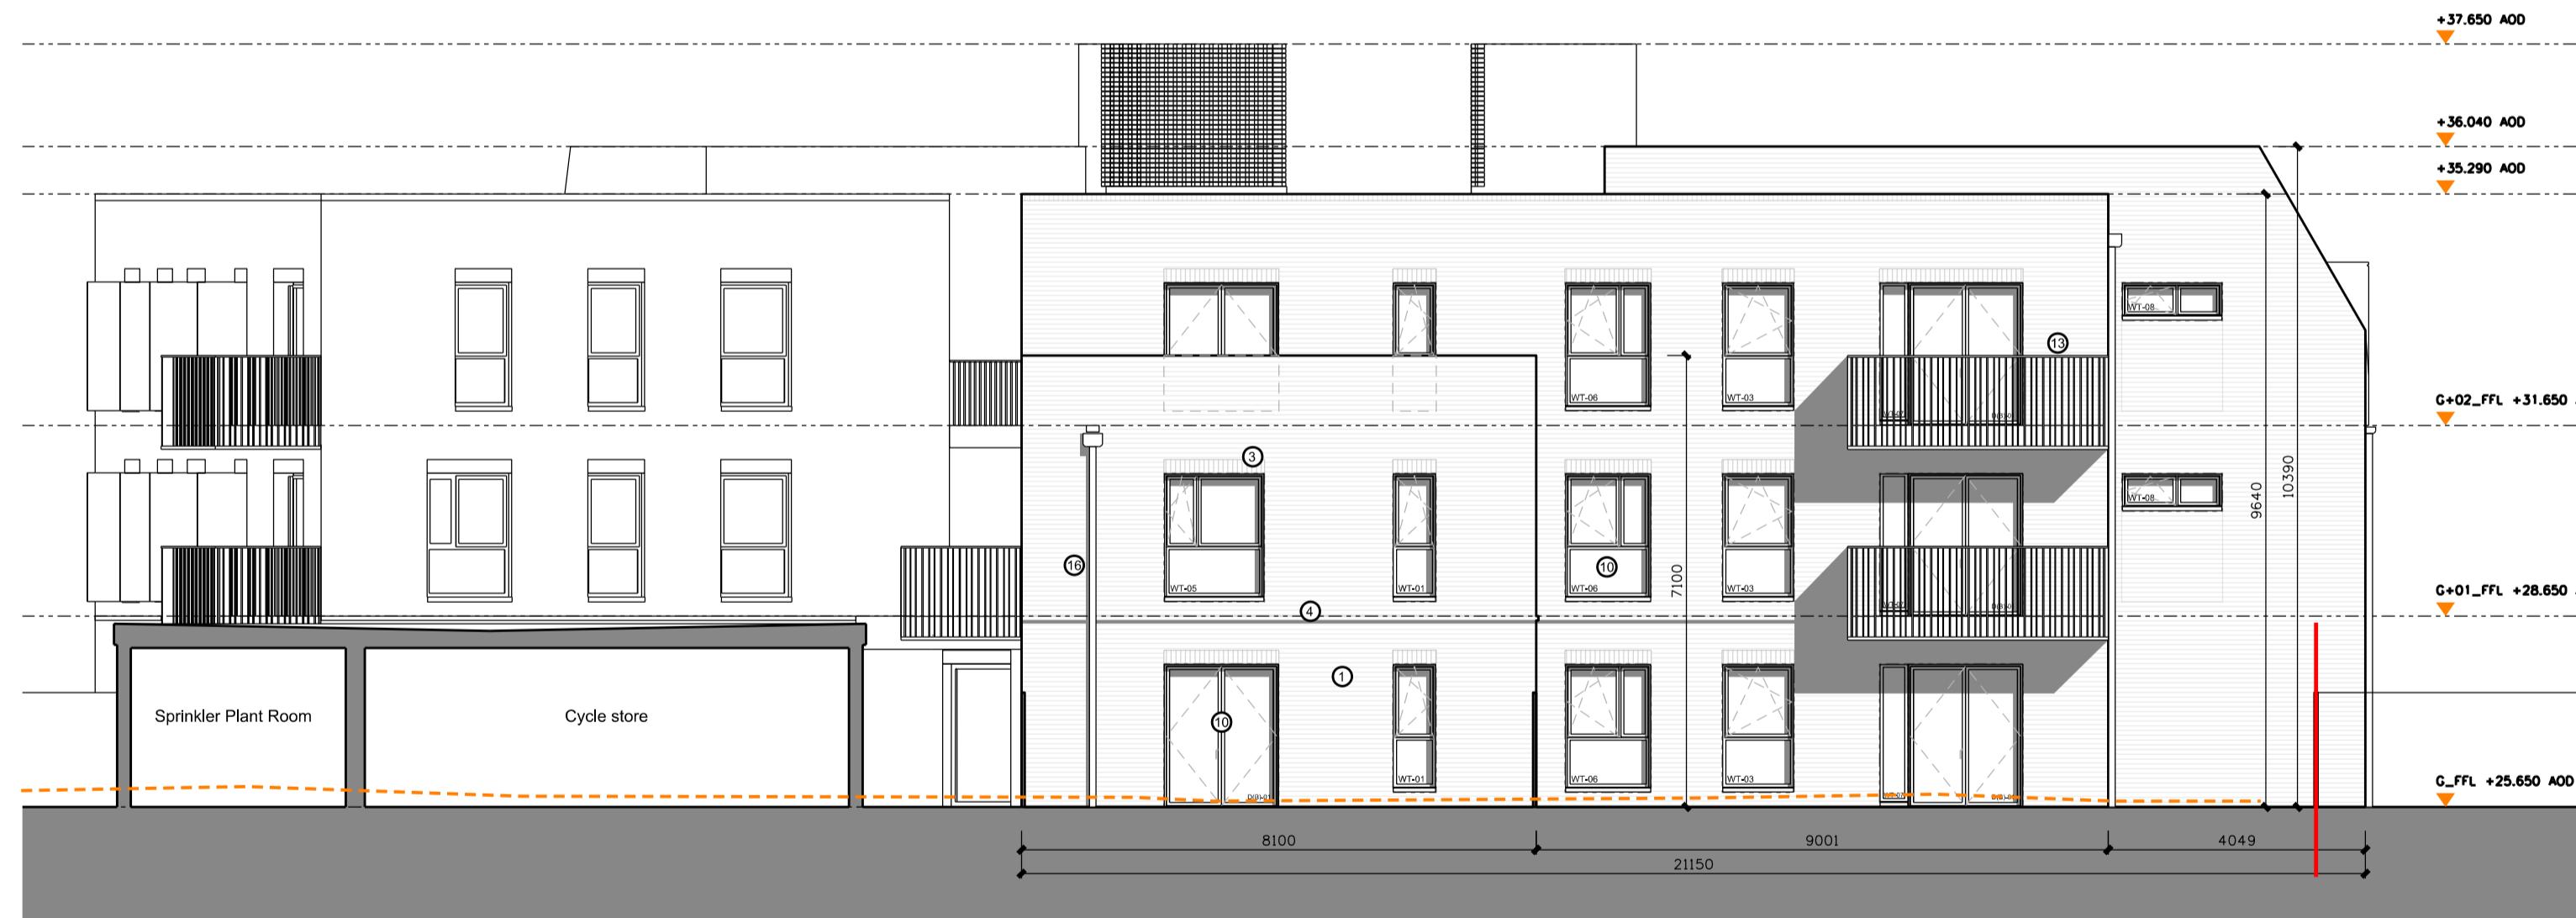

Elevation BF\_03



Elevation BF\_04

\* Landscaping omitted for clarity

Butterfly Building Elevations North Wing


0 1m 5m 10m  
1:100 @ A1

Revision	Date	Description	By	Check	Client logo
<b>Draft planning issue</b> <b>30/06/21</b>					

**Notes**  
Do not scale drawings. All dimensions should be checked on site. Errors to be reported to architect. To be read in conjunction with all relevant architects services reports and drawings.  
Contractors, sub-contractors and suppliers must verify any critical dimensions on site prior to fabrication of any building element. Any discrepancies are to be reported to the architect.  
This drawing should be read in conjunction with all relevant specifications, engineers and specialists consultants information. Any discrepancies must be reported prior to installation.

**Key**

- 1. Main brick: Reddish/brown brick with light mortar
- 2. Red brick with light mortar
- 3. Soldier course bond brick
- 4. Protruding stretcher bond brick >20mm
- 5. Reindeer bond brickwork
- 6. Sawtooth bond brickwork
- 7. Brick arch lintel, header bond
- 8. Clay pavers - terracotta red colour
- 9. Brown glazed brick sill
- 10. Brown glazed brick head
- 11. Aluminium composite window/door - RAL 6013 or similar
- 12. Dormer window surround - RAL 2001 or similar
- 13. Balcony metal frame - RAL 2001 or similar
- 14. Balcony PPC metal solid balustrade - RAL 2001 or similar
- 15. Canopy PPC metal - RAL 2001 or similar
- 16. Downwater pipe/piping - RAL 2001 or similar
- 17. Privacy screen - RAL 2001 or similar

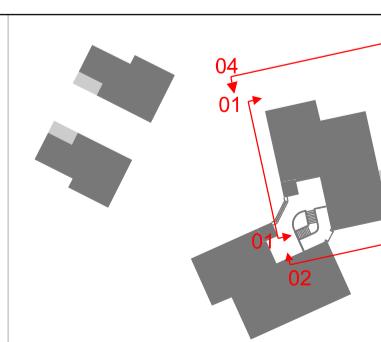


**Metropolitan Workshop**  
14-16 Cowcross Street  
London, EC1M 6DG  
+44 (0) 20 7566 0450  
www.metwork.co.uk

**Project:** Farmstead Road  
**Client:** Phoenix Community Housing  
**Location:** Farmstead Road, Bellingham, London  
**Title:** Butterfly Buildings Elevations\_North Wing  
**Date:** June 2021  
**Scale:** 1:100 @ A1  
**Drawing Number:** 1827  
**Status:** P  
**Package:** 102  
**Reference:** 101  
**Revision:** 00



Elevation BF\_05

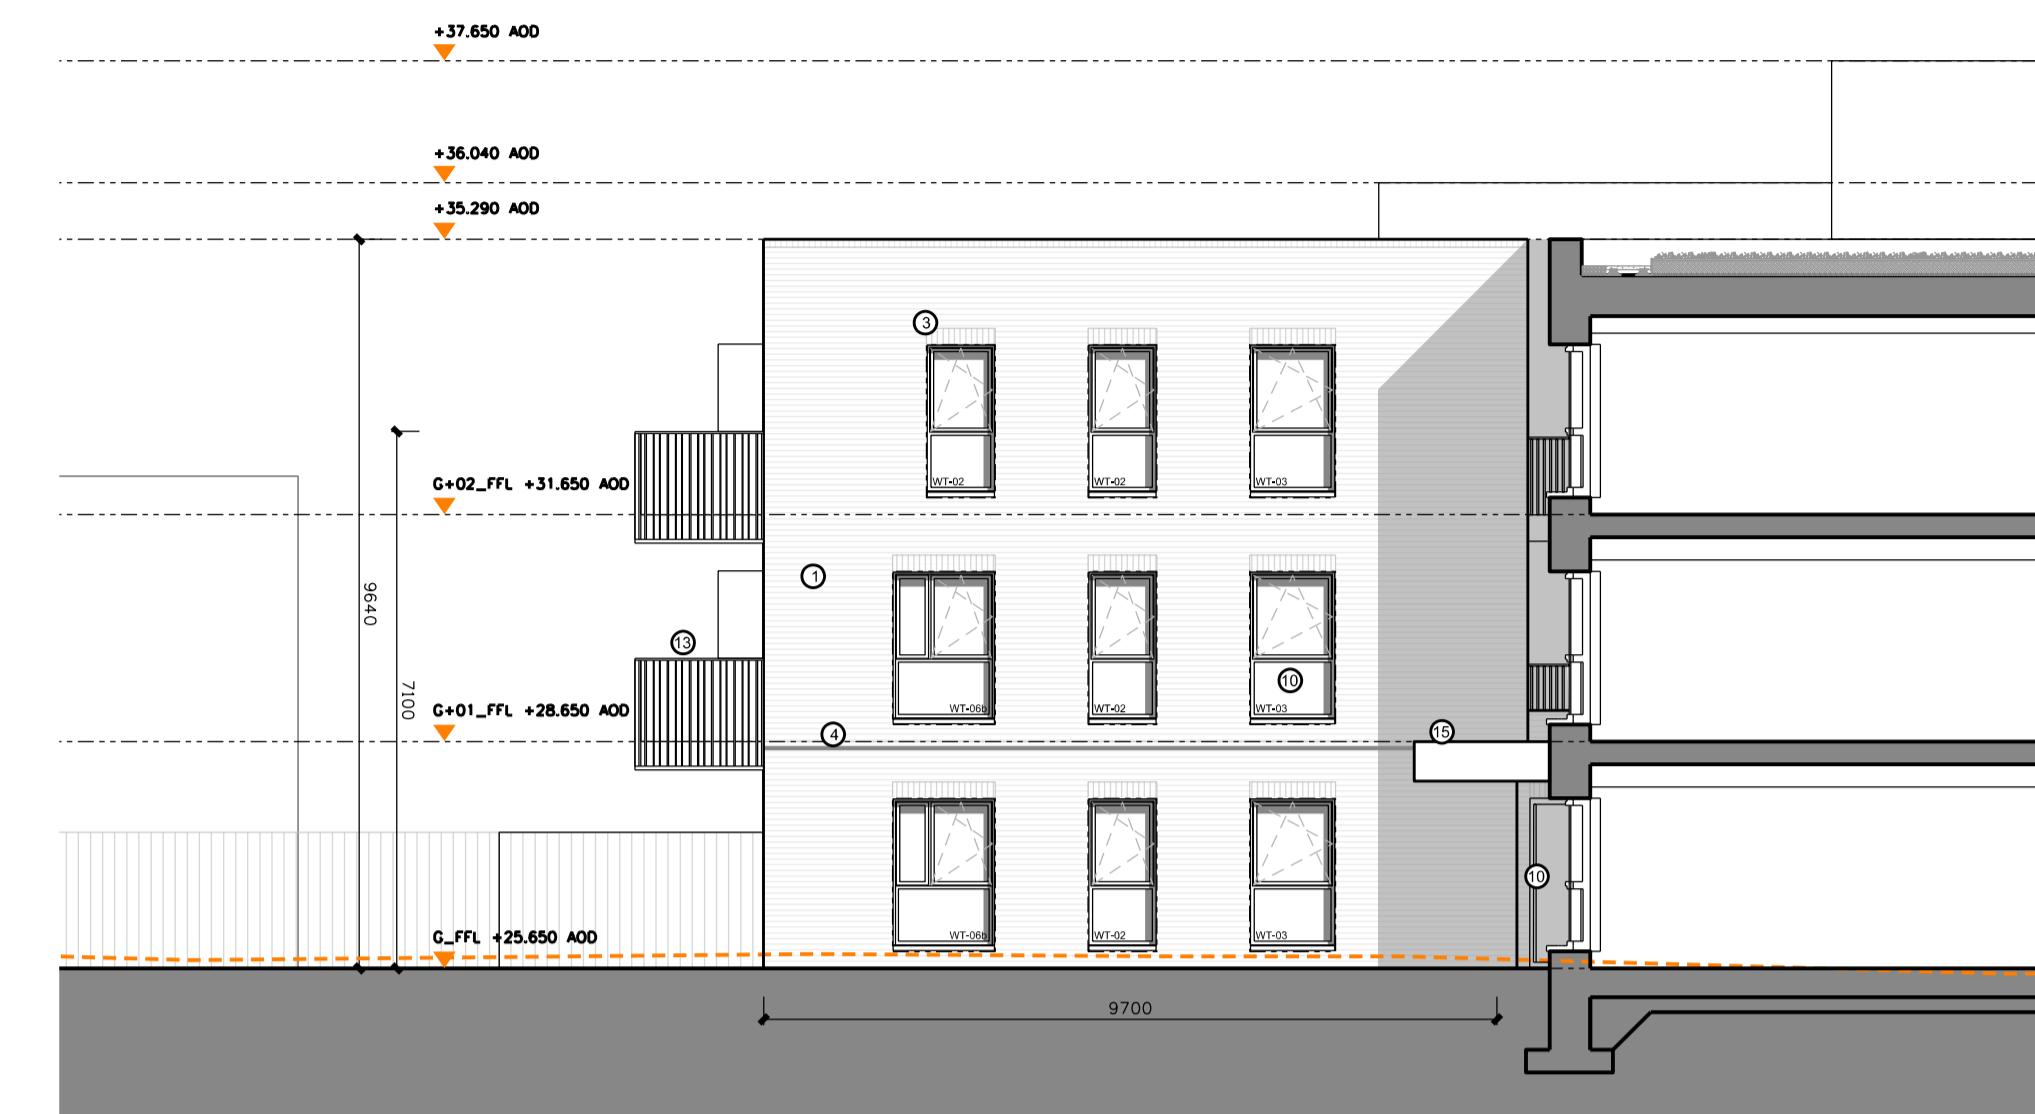

Elevation BF\_06



Elevation BF\_07



Elevation BF\_08

\* Landscaping omitted for clarity


#### Butterfly Building Elevations South Wing

0 1m 5m 10m  
1:100 @ A1

Revision	Date	Description	By	Check	Client logo
	30/06/21	Draft planning issue			Phoenix Our community in our hands

Notes  
Do not scale drawings. All dimensions should be checked on site. Errors to be reported to architect. To be read in conjunction with all relevant architects services drawings.  
Contractors, sub-contractors and suppliers must verify any critical dimensions on site prior to fabrication of any building element. Any discrepancies are to be reported to the architect.  
This drawing should be read in conjunction with all relevant specifications, engineers and specialists consultants information. Any discrepancies must be reported prior to installation.


Key  
1. Main brick: Reddish/brown brick with light mortar  
2. Brown glazed brick  
3. Soldier course bond brick  
4. Protruding stretcher bond brick >20mm  
5. Reindeer masonry bond  
6. Sawtooth bond brickwork  
7. Brick arch lintel, header bond  
8. Clay pavers - terracotta red colour  
9. Brown glazed brick sill  
10. Brown glazed brick window frame - RAL 2001 or similar  
11. Aluminium composite window/door - RAL 6013 or similar  
12. Dormer window surround - RAL 2001 or similar  
13. Balcony metal solid balustrade - RAL 2001 or similar  
14. Balcony PPC metal solid balustrade - RAL 2001 or similar  
15. Canopy PPC metal solid balustrade - RAL 2001 or similar  
16. Downwater pipe/piping - RAL 2001 or similar  
17. Privacy screen - RAL 2001 or similar

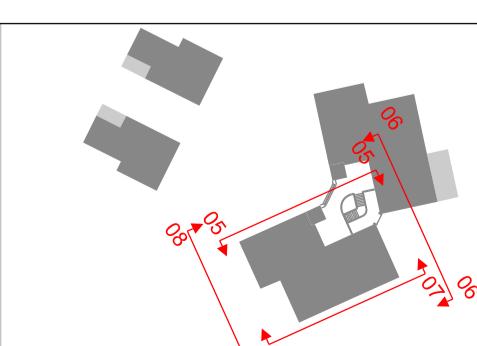


Metropolitan  
Workshop

14-16 Cowcross Street  
London, EC1M 6DG  
+44 (0) 20 7566 0450  
www.metwork.co.uk


Project:	Farmstead Road
Client:	Phoenix Community Housing
Location:	Farmstead Road, Bellington, London
Title:	Butterfly Buildings Elevations_South Wing
Date:	June 2021
Scale:	1:100 @ A1
Drawing Number:	1827
Job No.	P
Status	102
Package	102
Reference	00
Revision	

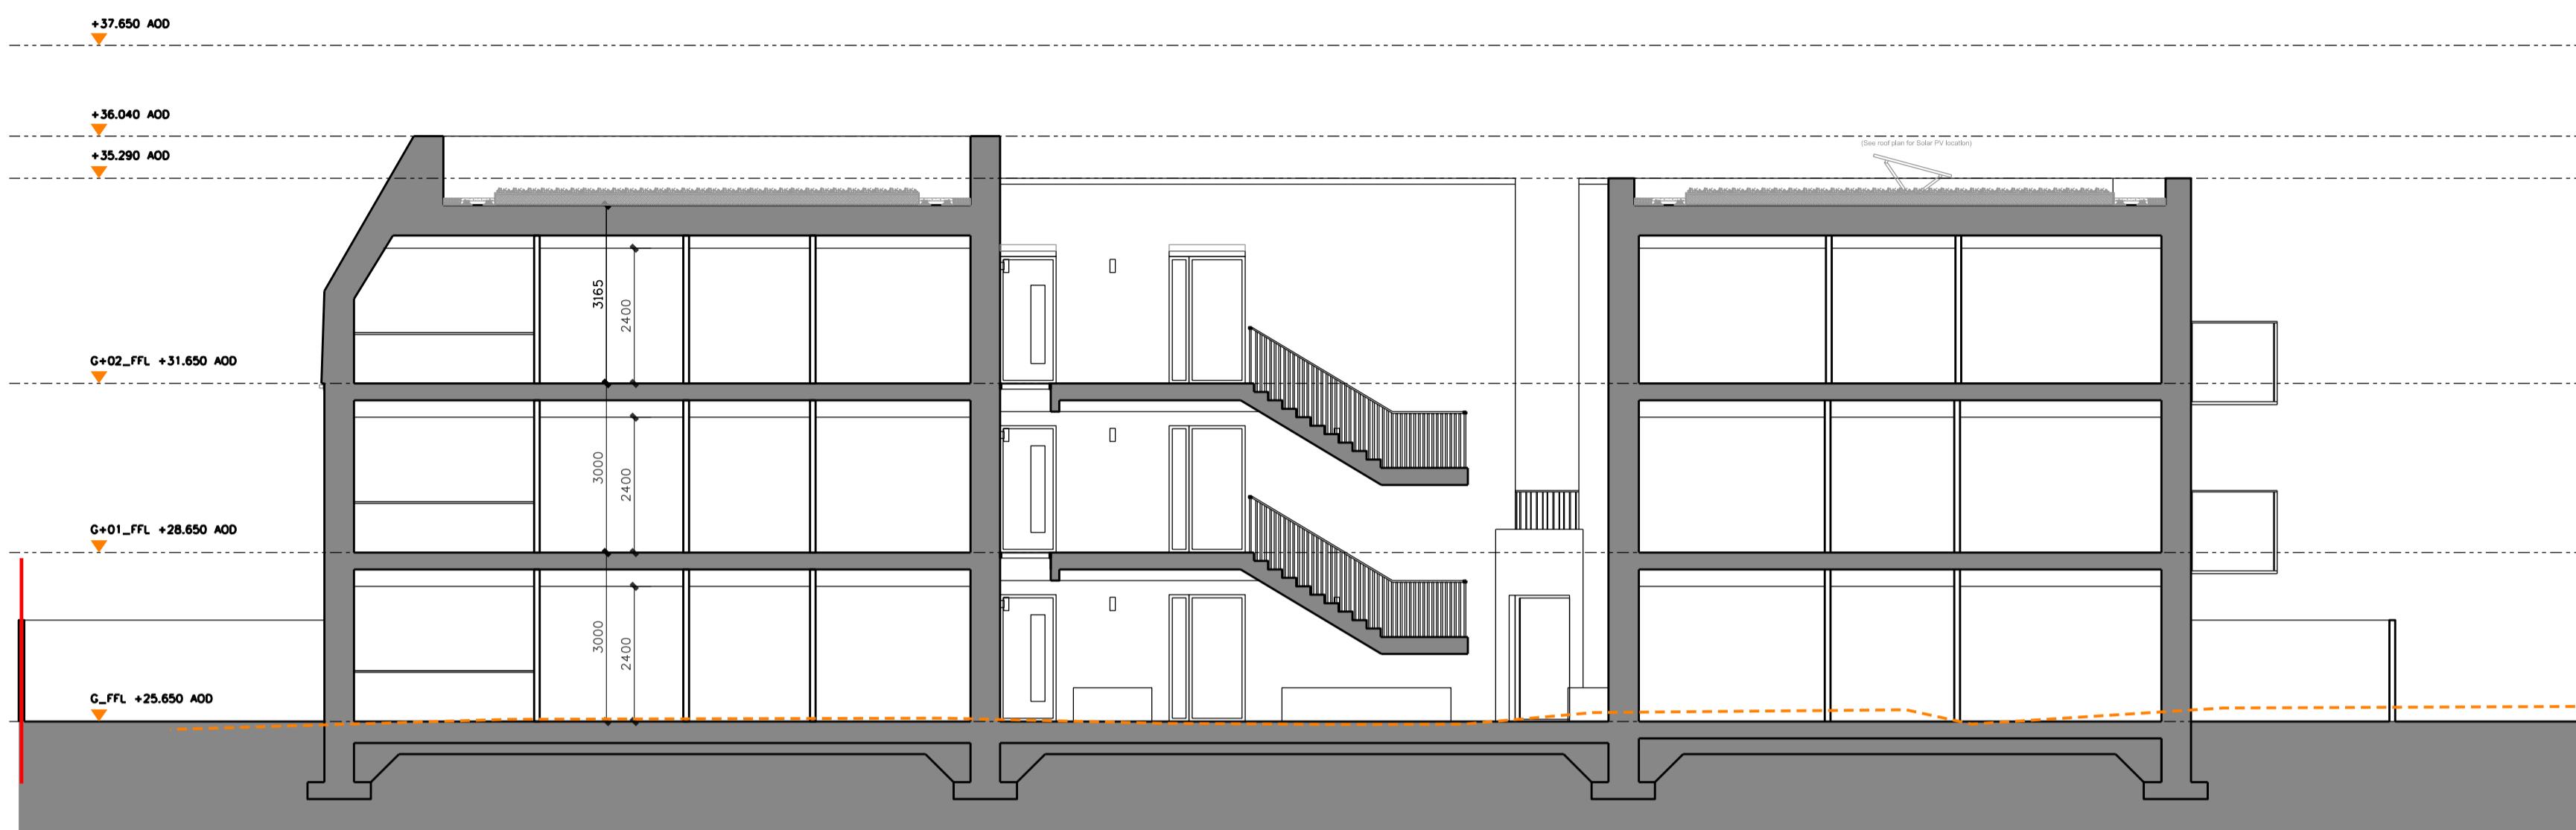


Section BF\_AA

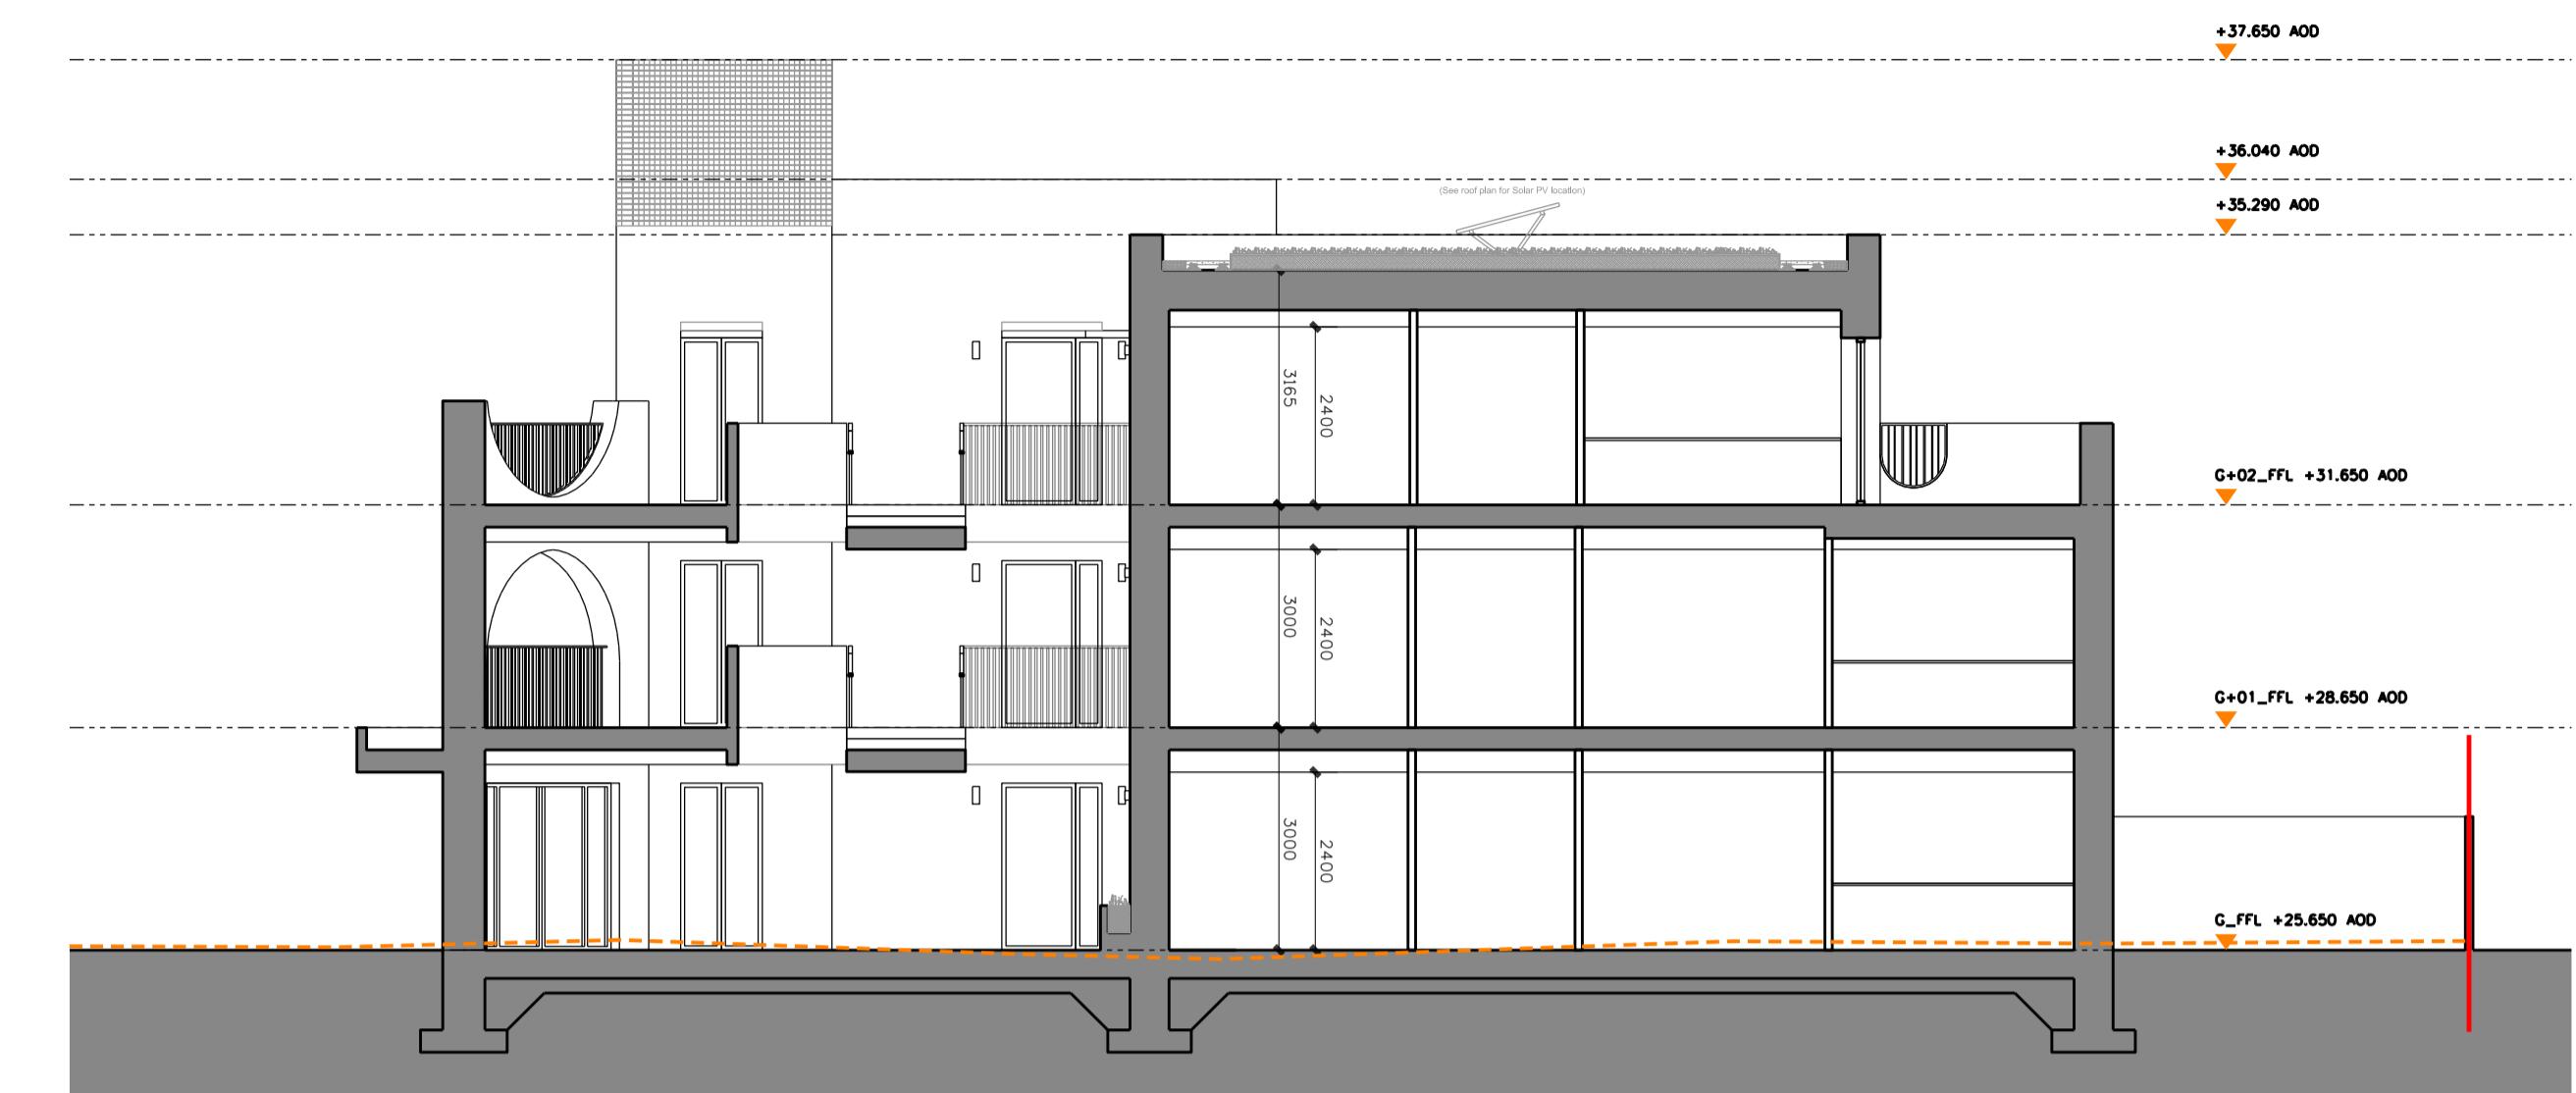

Section BF\_BB

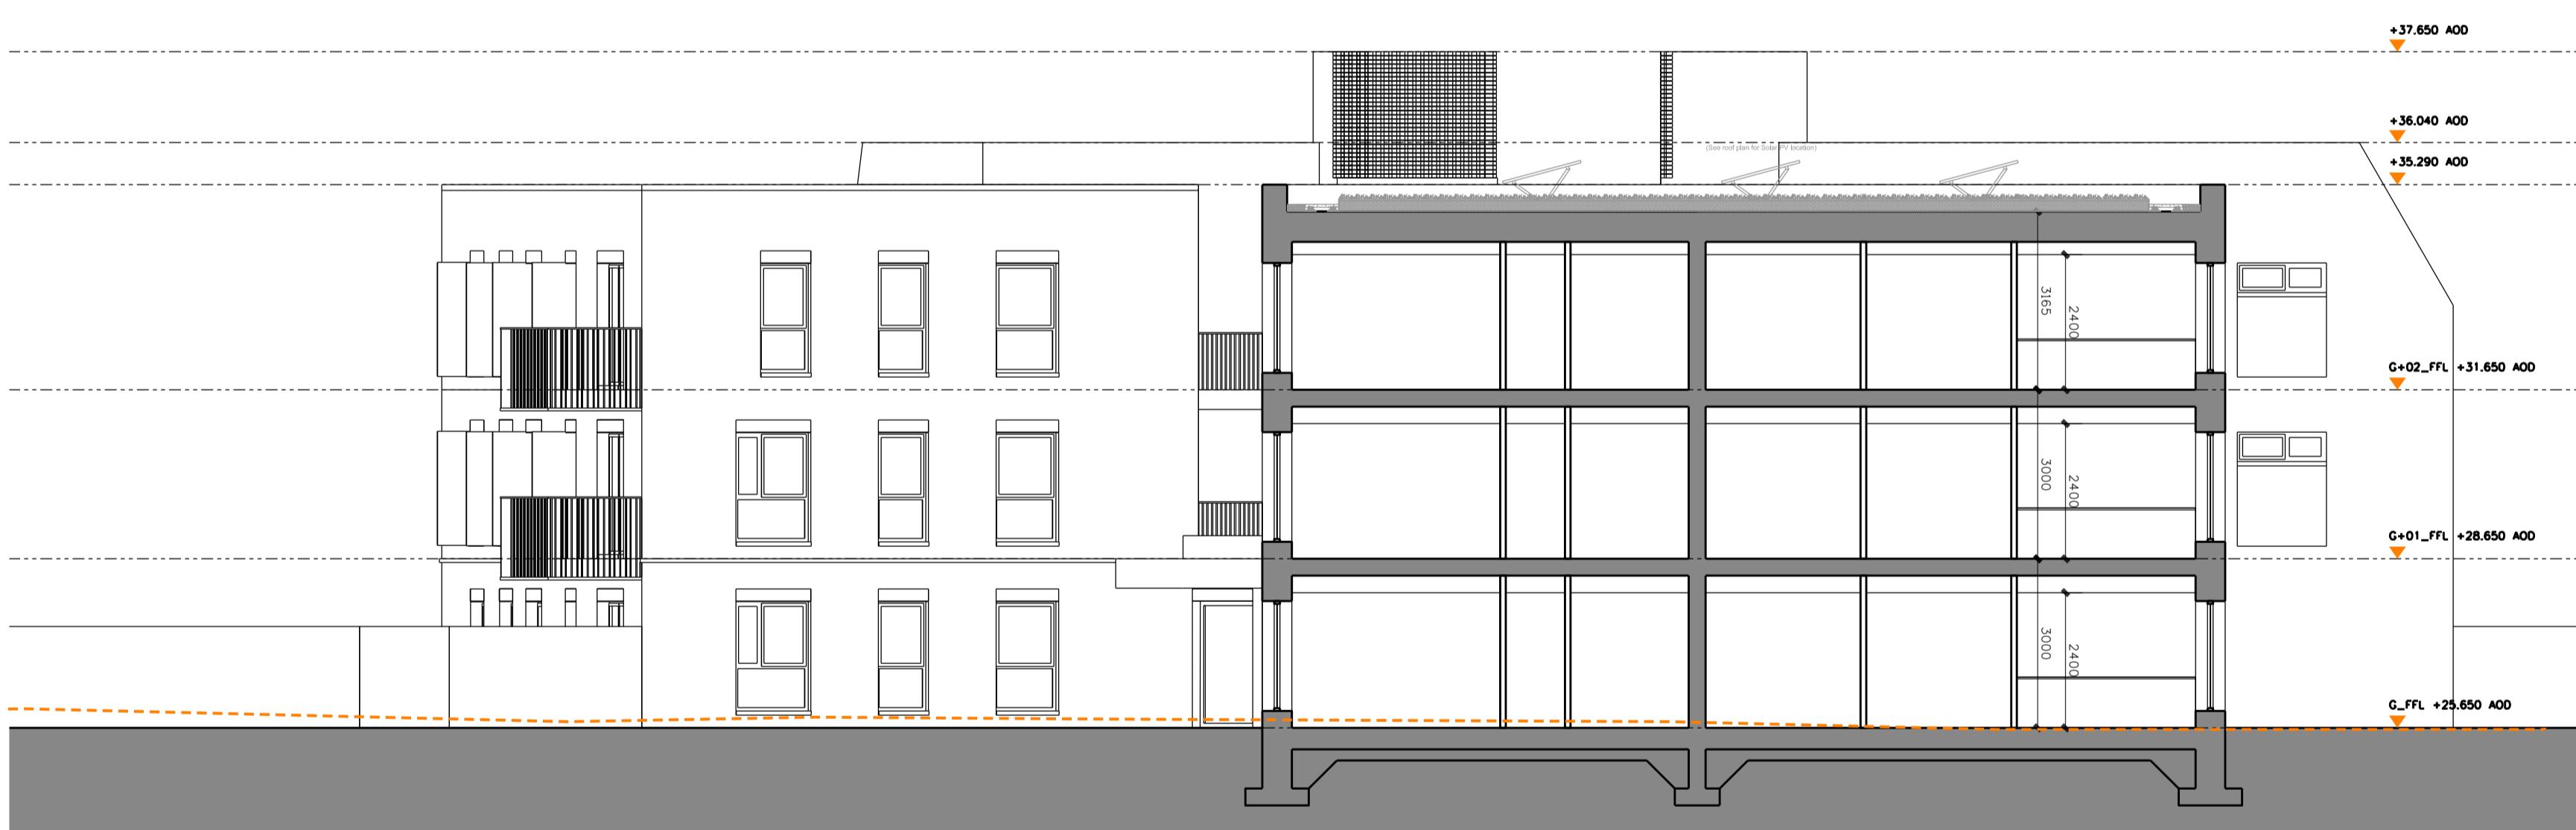

Section BF\_CC

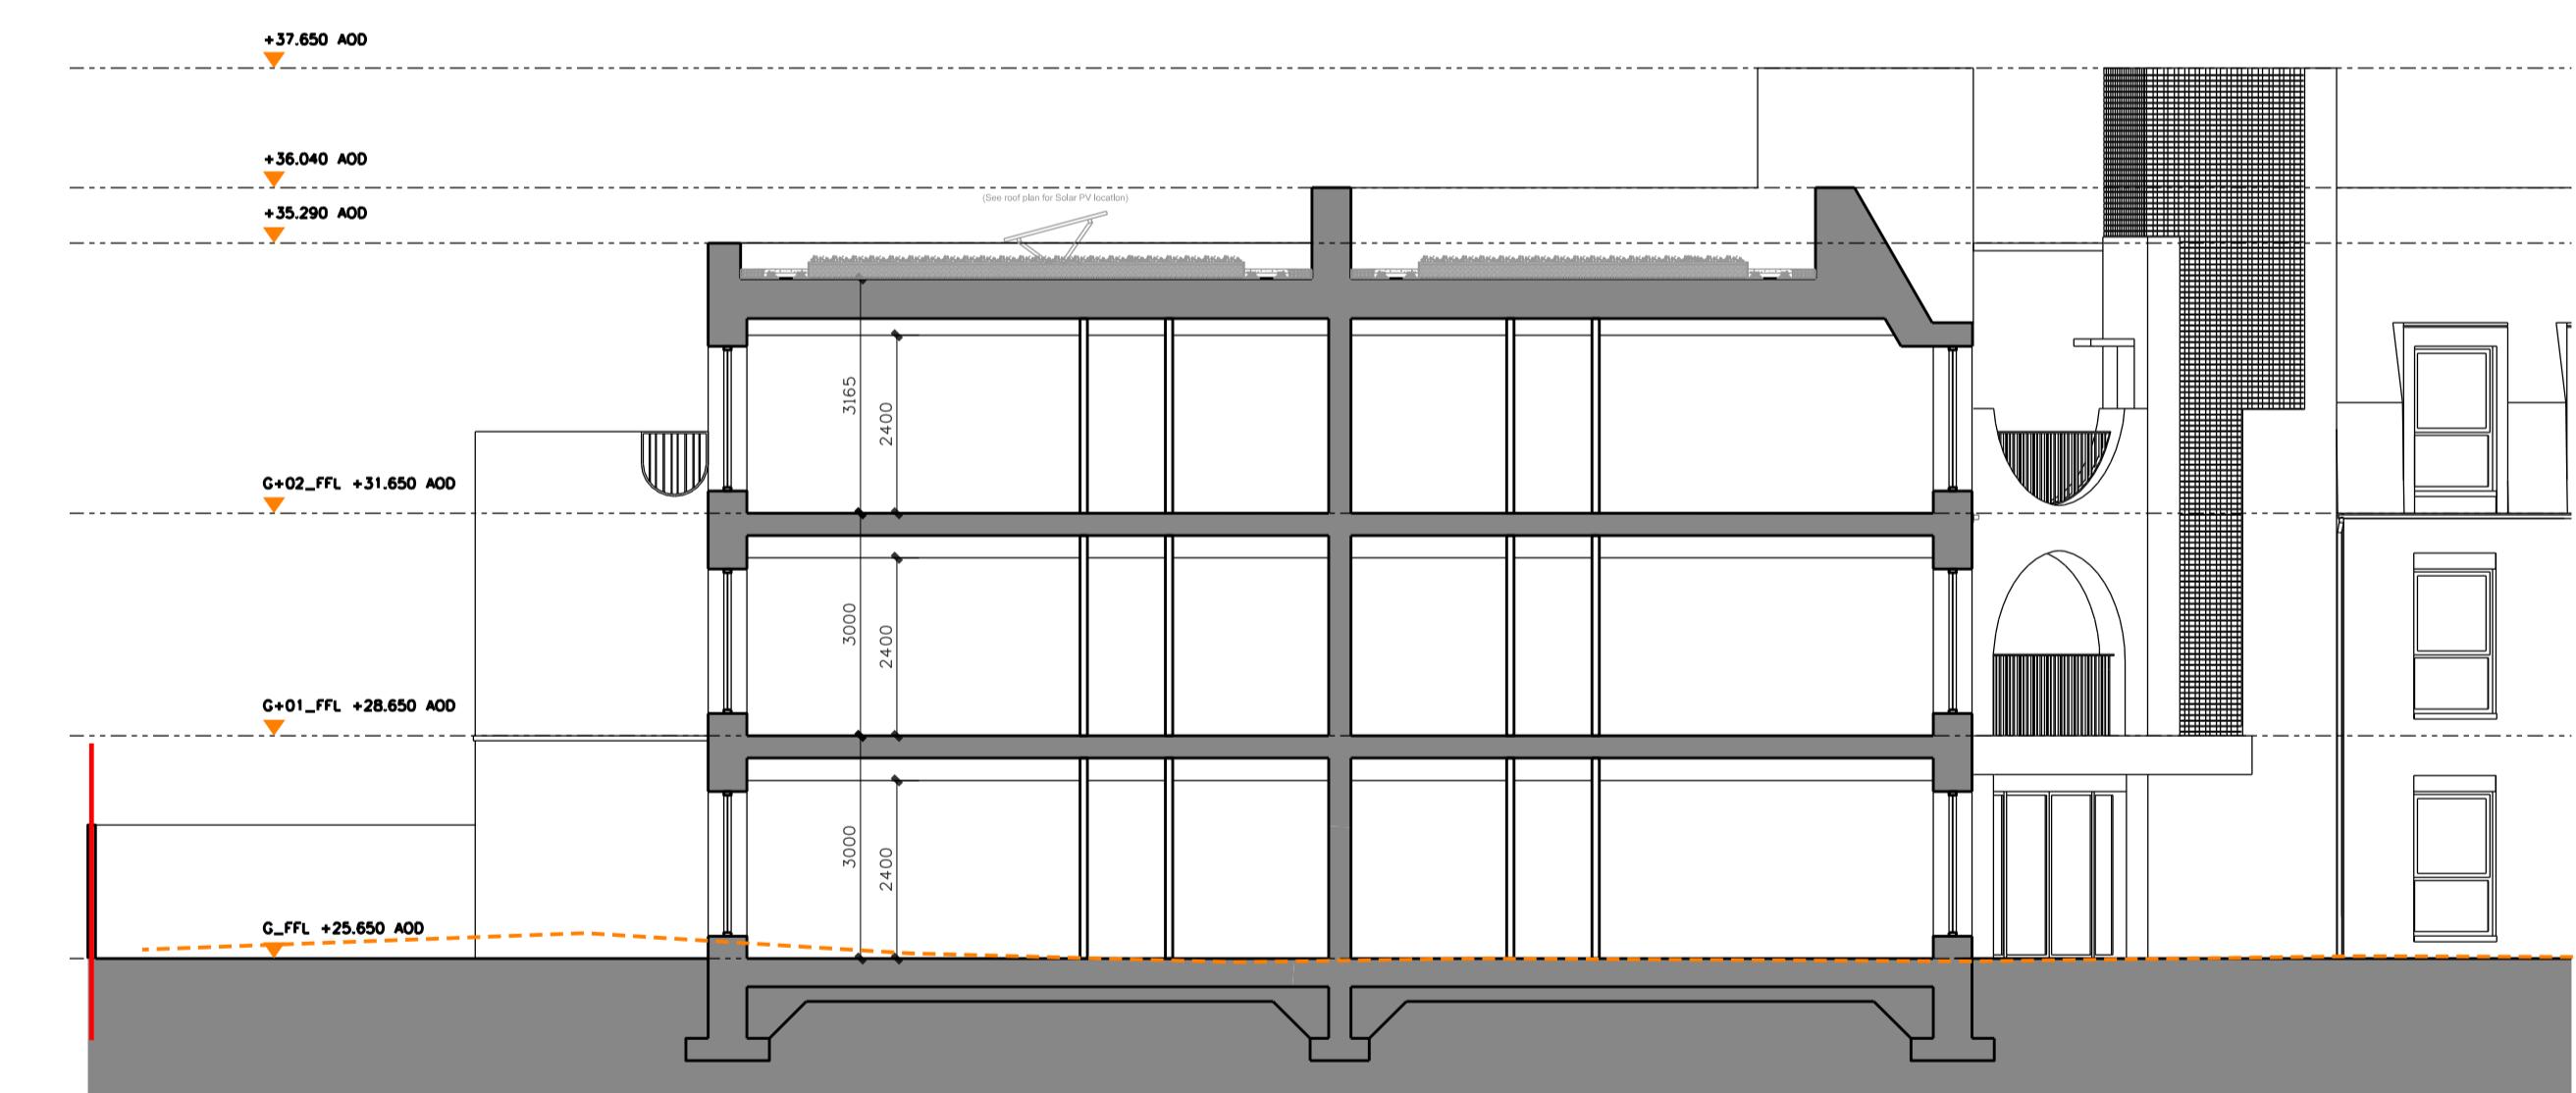

Section BF\_DD

\* Landscaping omitted for clarity


Butterfly Building Sections North Wing

0 1m 5m 10m  
1:100 @ A1

Revision	Date	Description	By	Check	Client logo
<b>Draft planning issue</b> <b>30/06/21</b>					

Notes  
Do not scale drawings. All dimensions should be checked on site. Errors to be reported to architect. To be read in conjunction with all relevant architects services drawings.  
Contractors, sub-contractors and suppliers must verify any critical dimensions on site prior to fabrication of any building element. Any discrepancies are to be reported to the architect.  
This drawing should be read in conjunction with all relevant specifications, engineers and specialists consultants information. Any discrepancies must be reported prior to installation.


Key

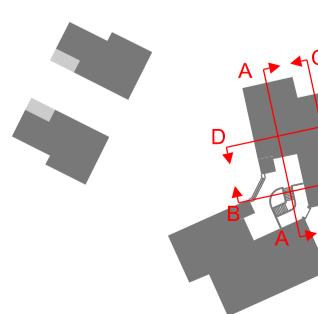


**Metropolitan Workshop**

14-16 Cowcross Street  
London, EC1M 6DG  
+44 (0) 20 7566 0450  
www.metwork.co.uk


Project:	Farmstead Road
Client:	Phoenix Community Housing
Location:	Farmstead Road, Bellingham, London
Title:	Butterfly Buildings Sections_North Wing
Date:	June 2021
Scale:	1:100 @ A1
Drawing Number:	1827 P 103 101 00

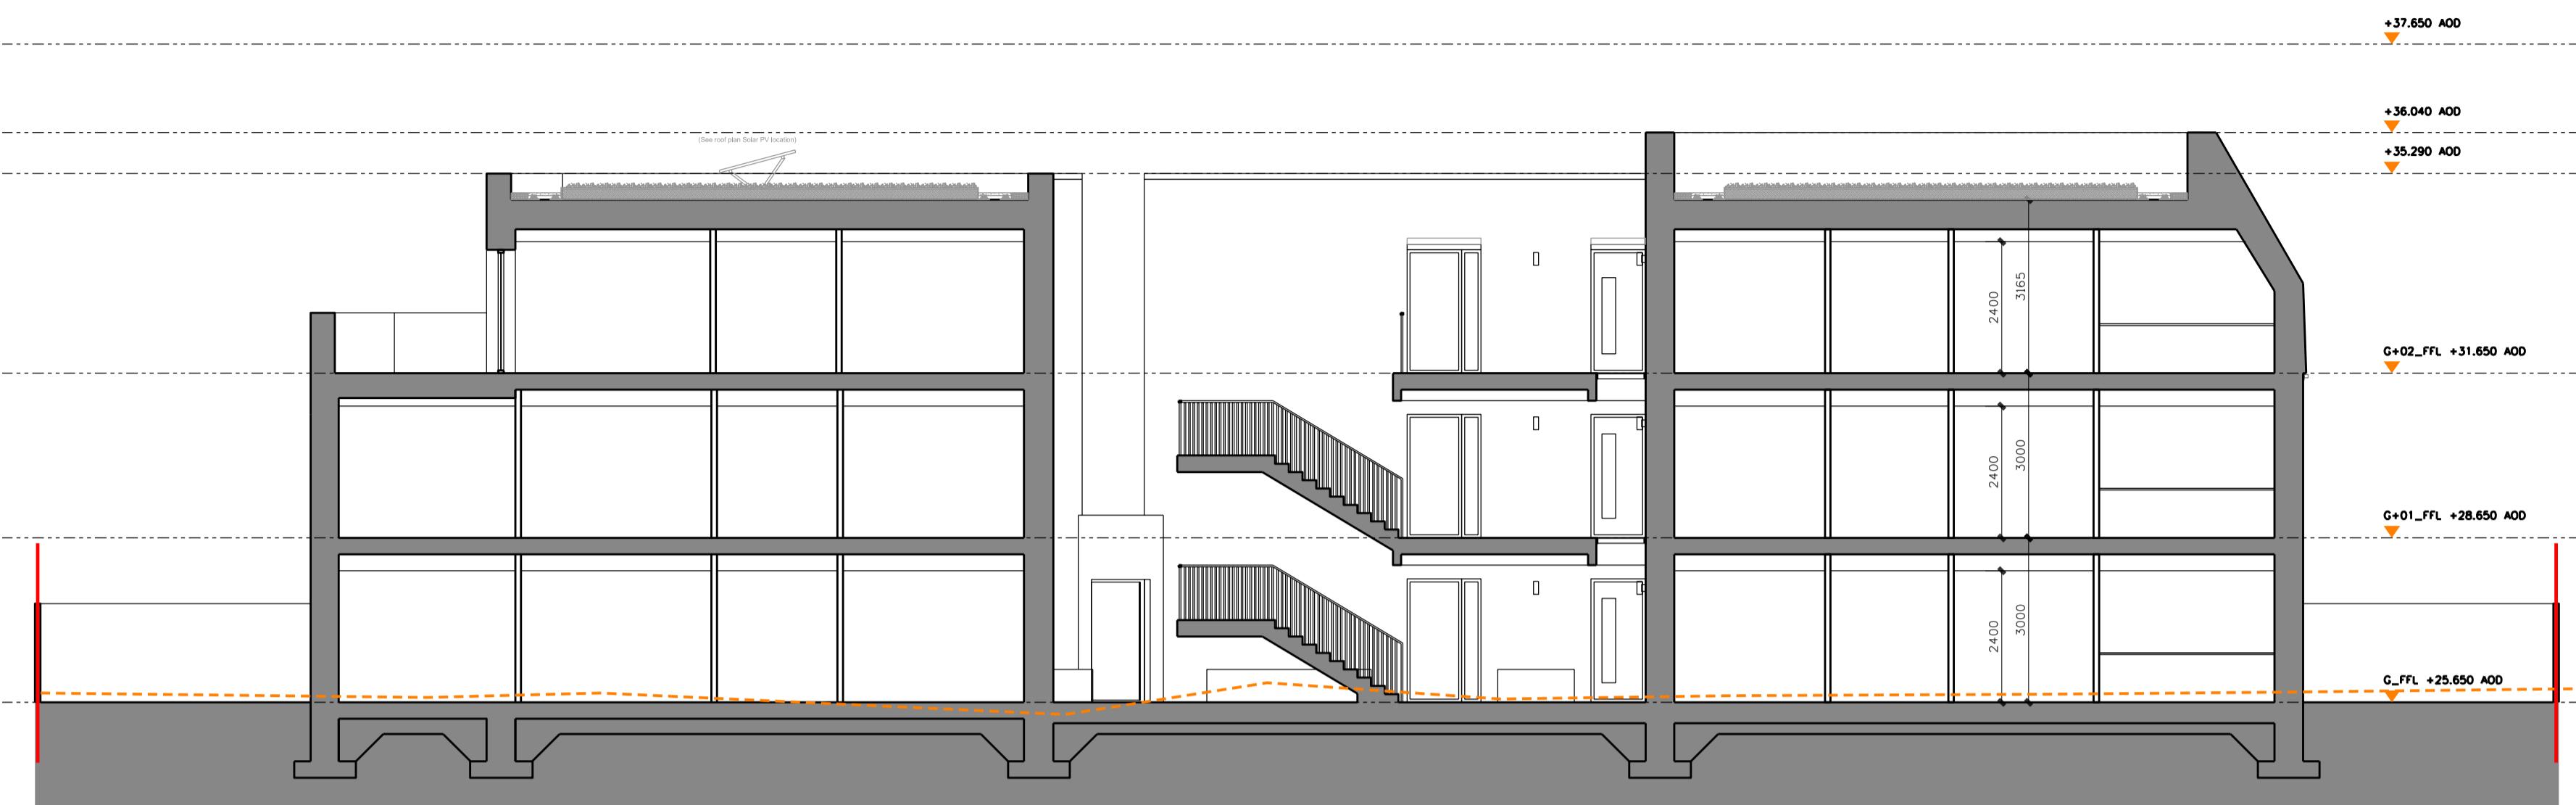


Section BF\_EE

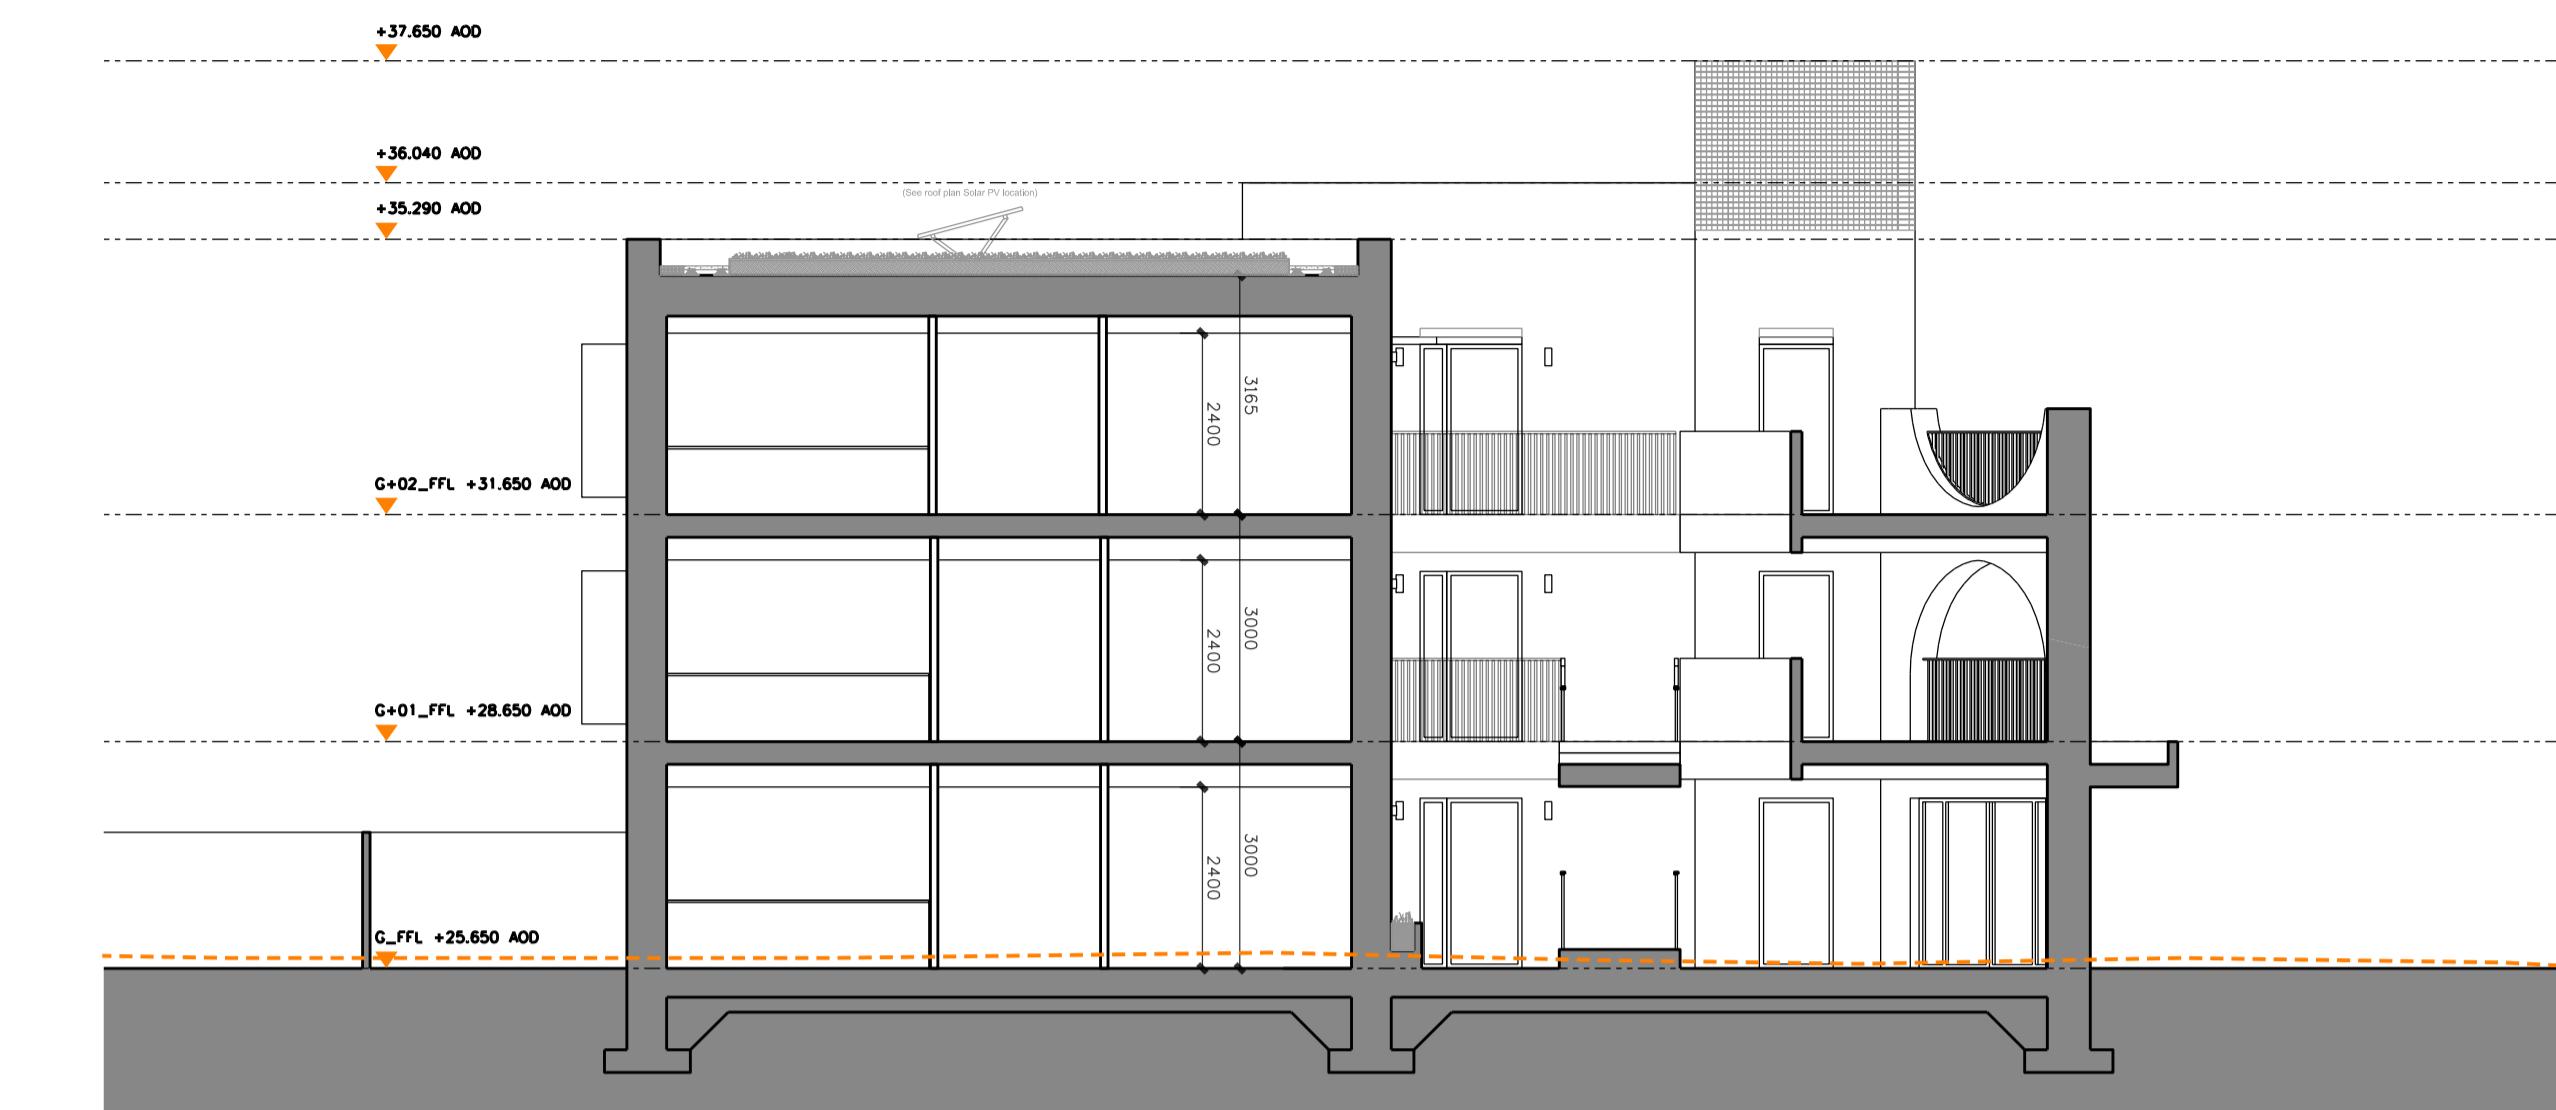

Section BF\_FF

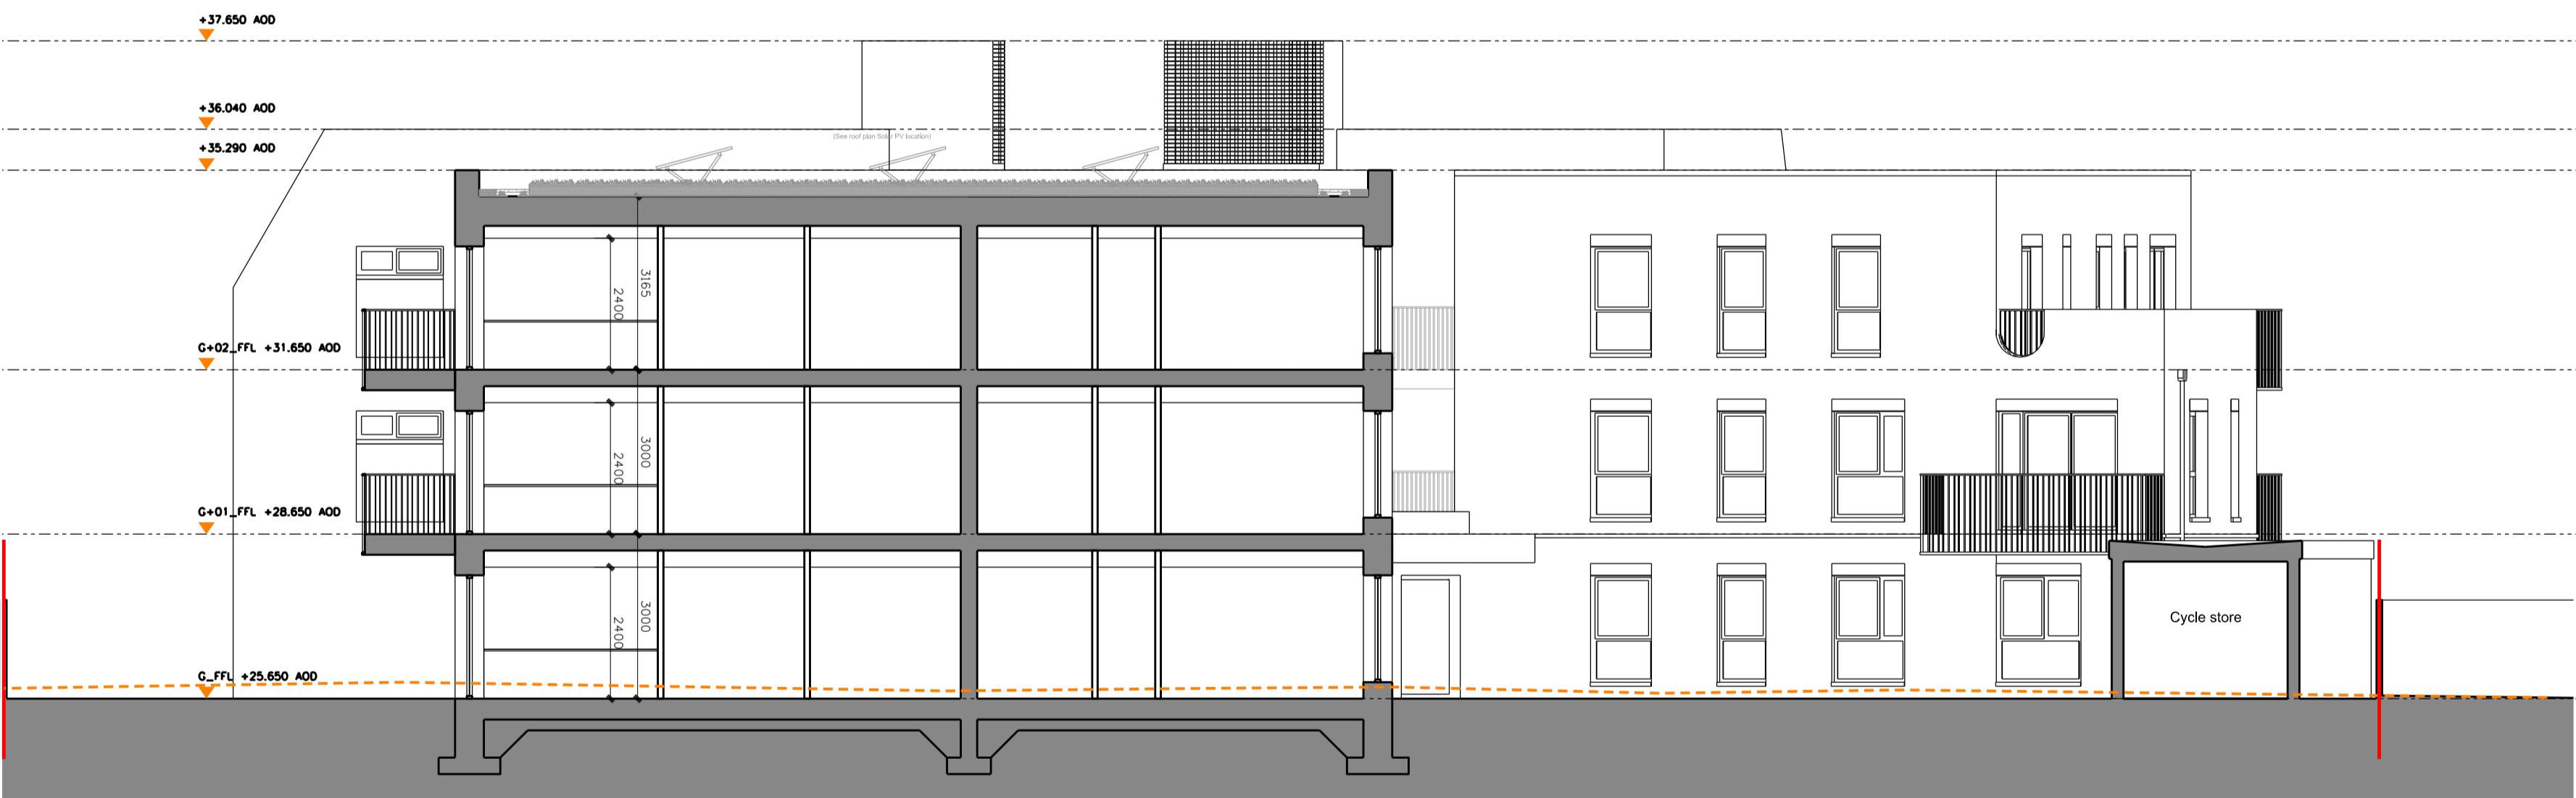

Section BF\_GG

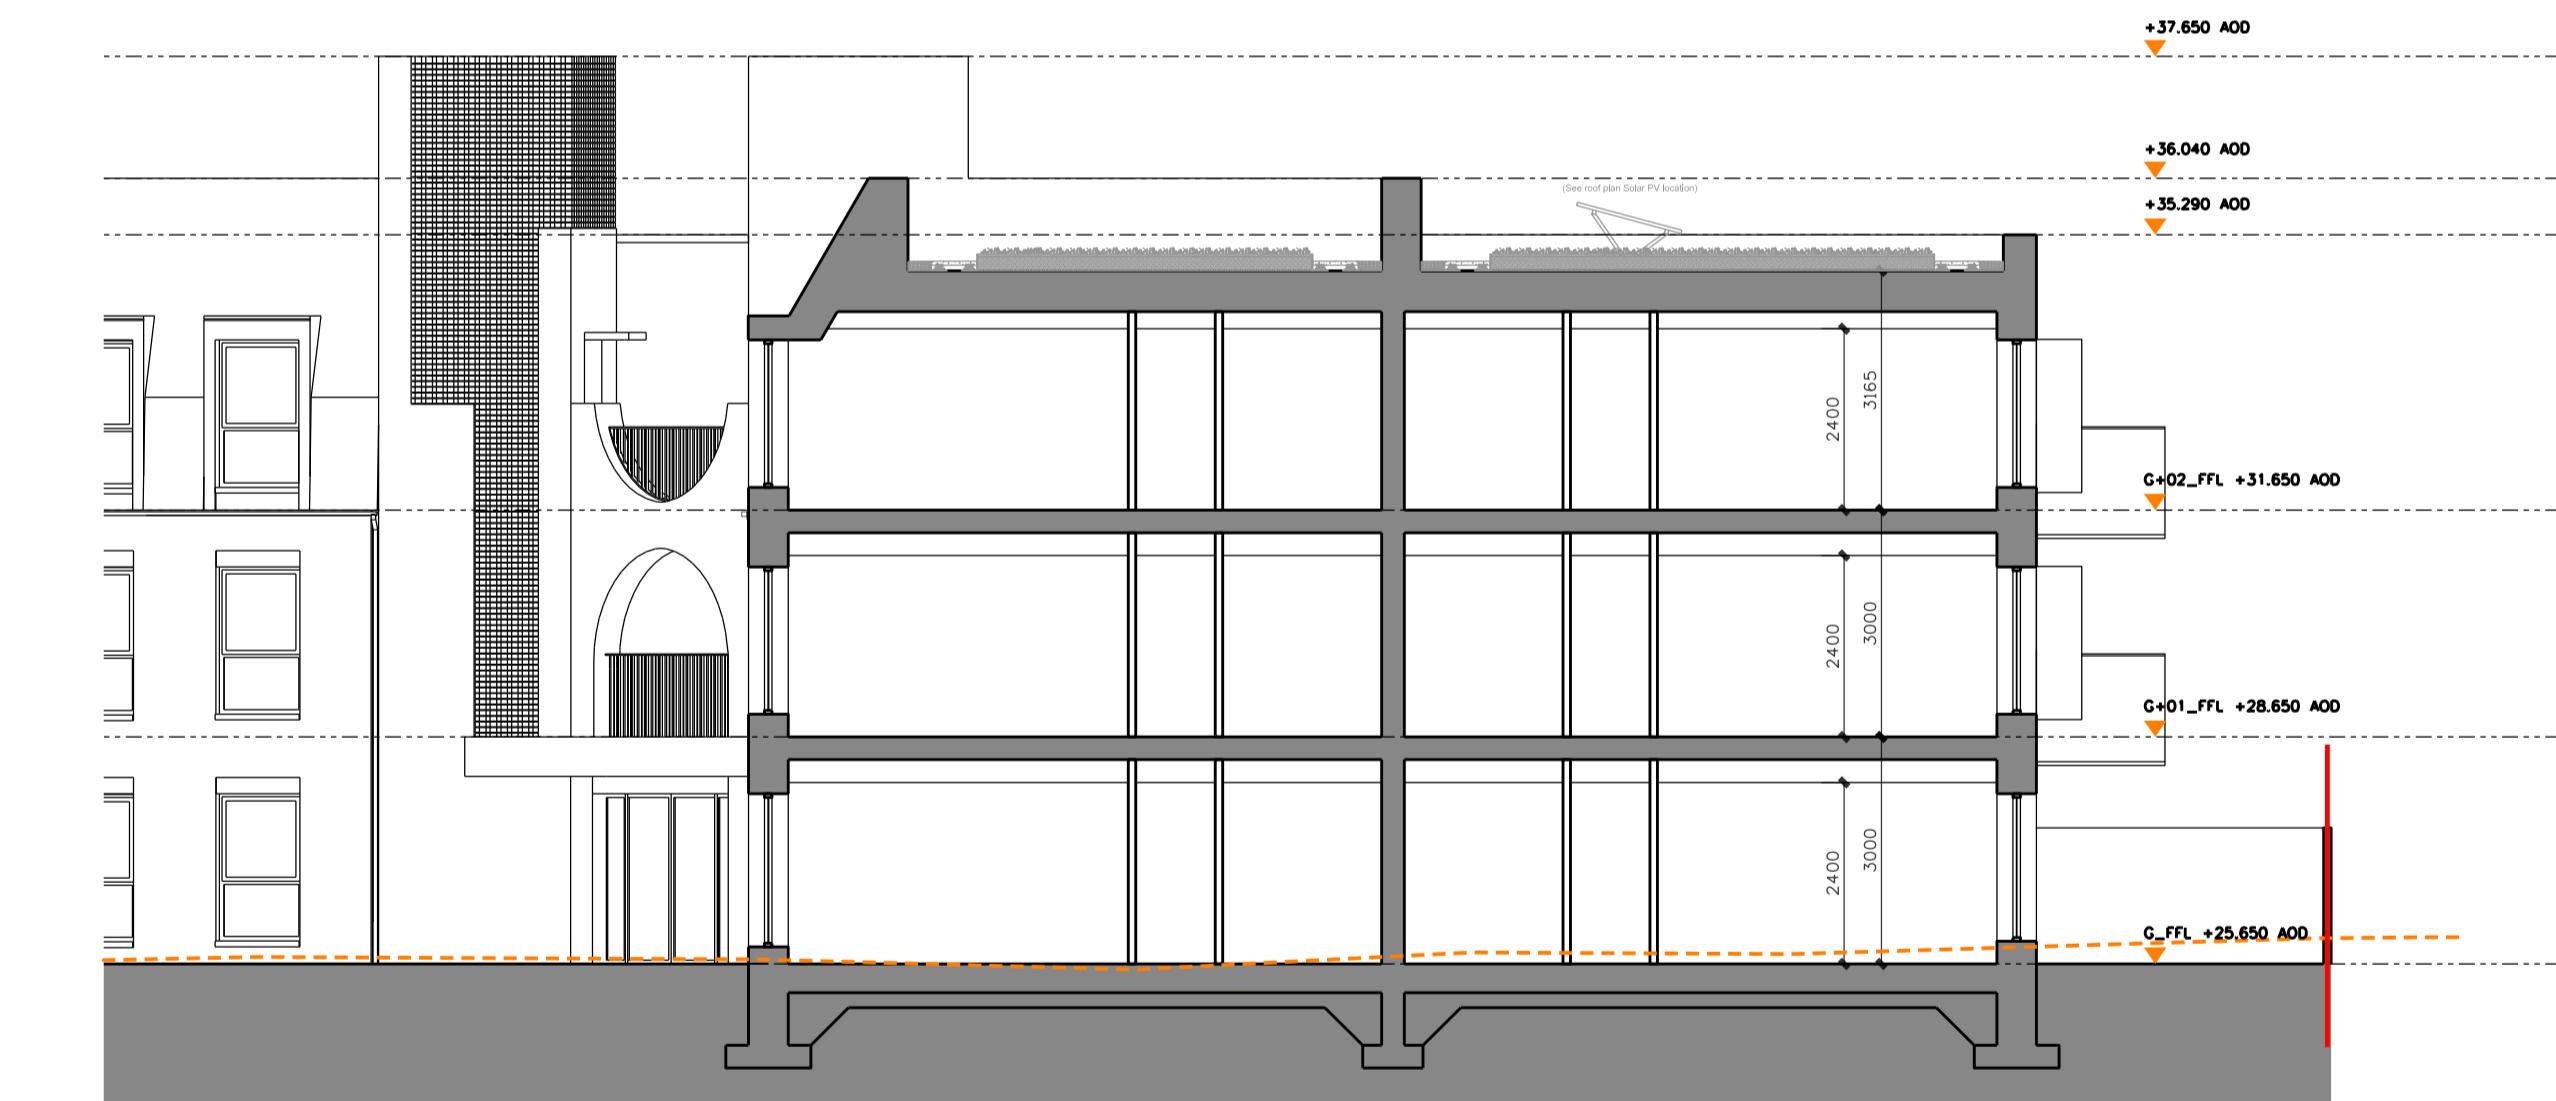

Section BF\_HH

\* Landscaping omitted for clarity


Butterfly Building Sections South Wing

0 1m 5m 10m  
1:100 @ A1

Revision	Date	Description	By	Check	Client logo
<b>Draft planning issue</b> <b>30/06/21</b>					

Notes  
Do not scale drawings. All dimensions should be checked on site. Errors to be reported to architect. To be read in conjunction with all relevant architects services drawings.  
Contractors, sub-contractors and suppliers must verify any critical dimensions on site prior to fabrication of any building element. Any discrepancies are to be reported to the architect.  
This drawing should be read in conjunction with all relevant specifications, engineers and specialists consultants information. Any discrepancies must be reported prior to installation.

Key

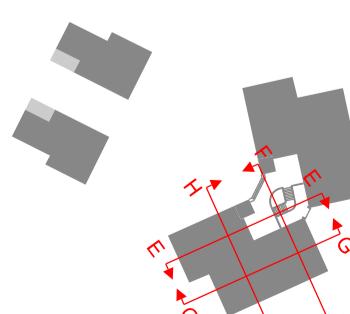

**Metropolitan Workshop**

14-16 Cowcross Street  
London, EC1M 6DG  
+44 (0) 20 7566 0450  
www.metwork.co.uk

Project:	Farmstead Road
Client:	Phoenix Community Housing
Location:	Farmstead Road, Bellingham, London
Title:	Butterfly Buildings_South Wing
Date:	June 2021
Scale:	1:100 @ A1
Drawing Number:	1827 P 103 102 00



Site Elevation 01



Site Elevation 02



Site Elevation 03

Proposed Site Elevations

Scale: mm

By:

Check:

Client logo:




Notes:

On no scale drawings. All dimensions should be checked on site. Errors to be reported to architect. To be read in conjunction with all relevant architects services and other drawings issued by architect.

Contractors, subcontractors and suppliers must verify any critical dimensions on site prior to fabrication of any building element. Any discrepancies are to be reported to architect.

This drawing should be read in conjunction with all relevant specifications, engineers reports and manufacturers instructions. Any discrepancies must be reported prior to installation.

Key:

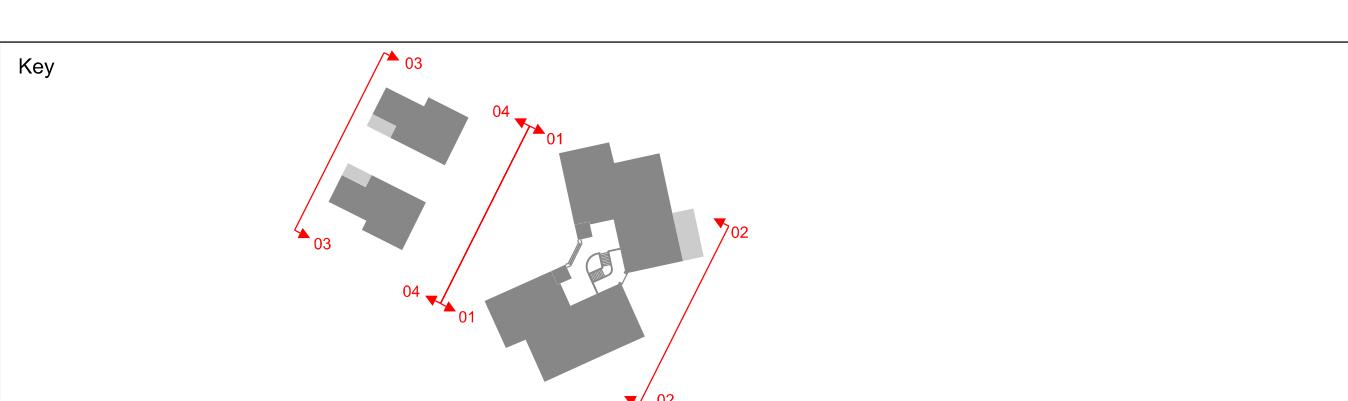

14-16 Cowcross Street  
London, EC1M 6DG  
+44 (0) 20 7566 0450  
www.metwork.co.uk

Project: Farmstead Road  
Client: Phoenix Community Housing  
Location: Farmstead Road, Bellington, London, SE6 3ED  
Title: Proposed Site Elevations  
Date: June 2021  
Scale: 1:100 @ A0


Drawing number: Job No. Status Package Reference Revision

1827 P 102 103 00


**Draft planning issue  
30/06/21**



Site Section 01

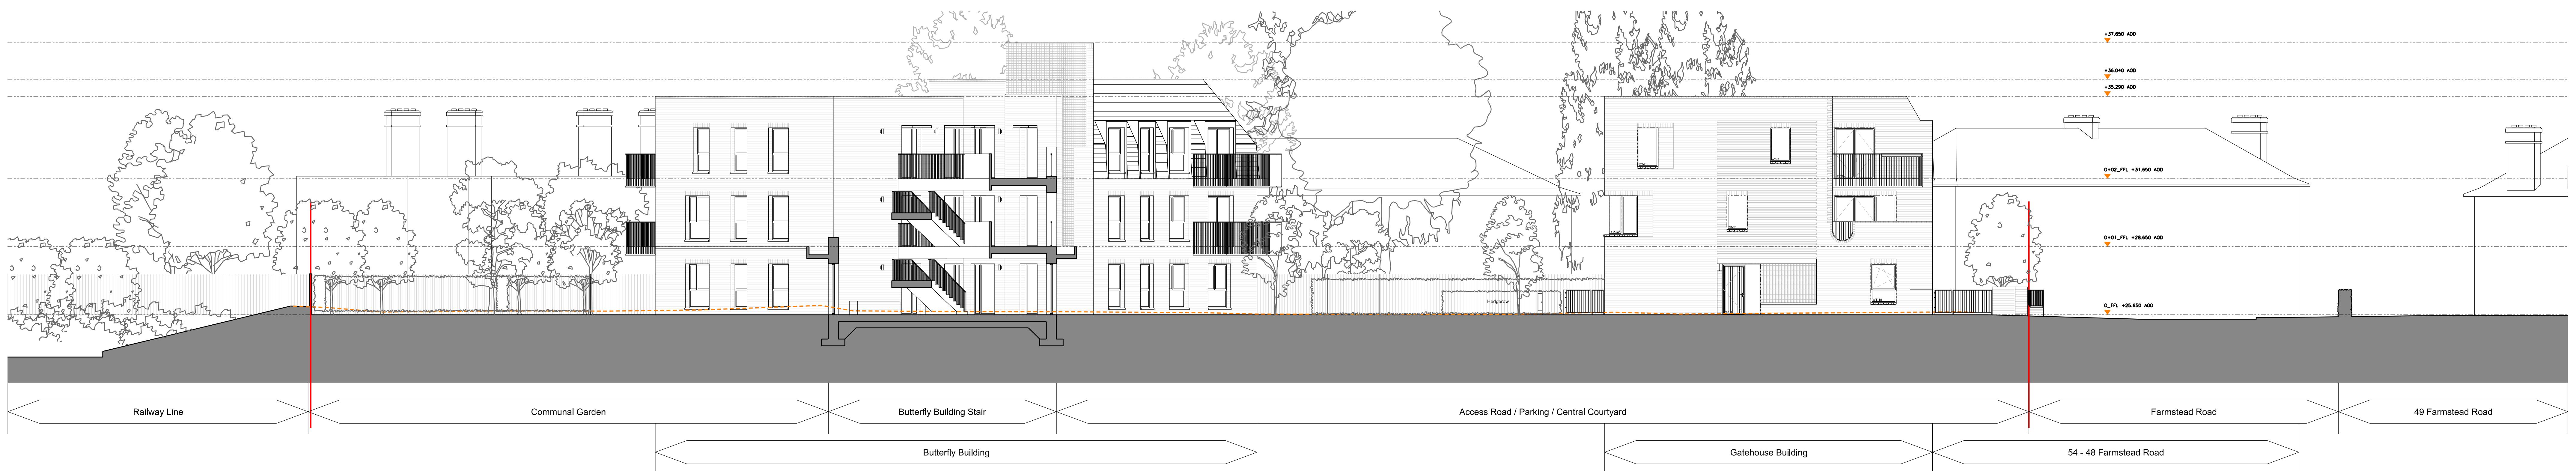

Site Section 02

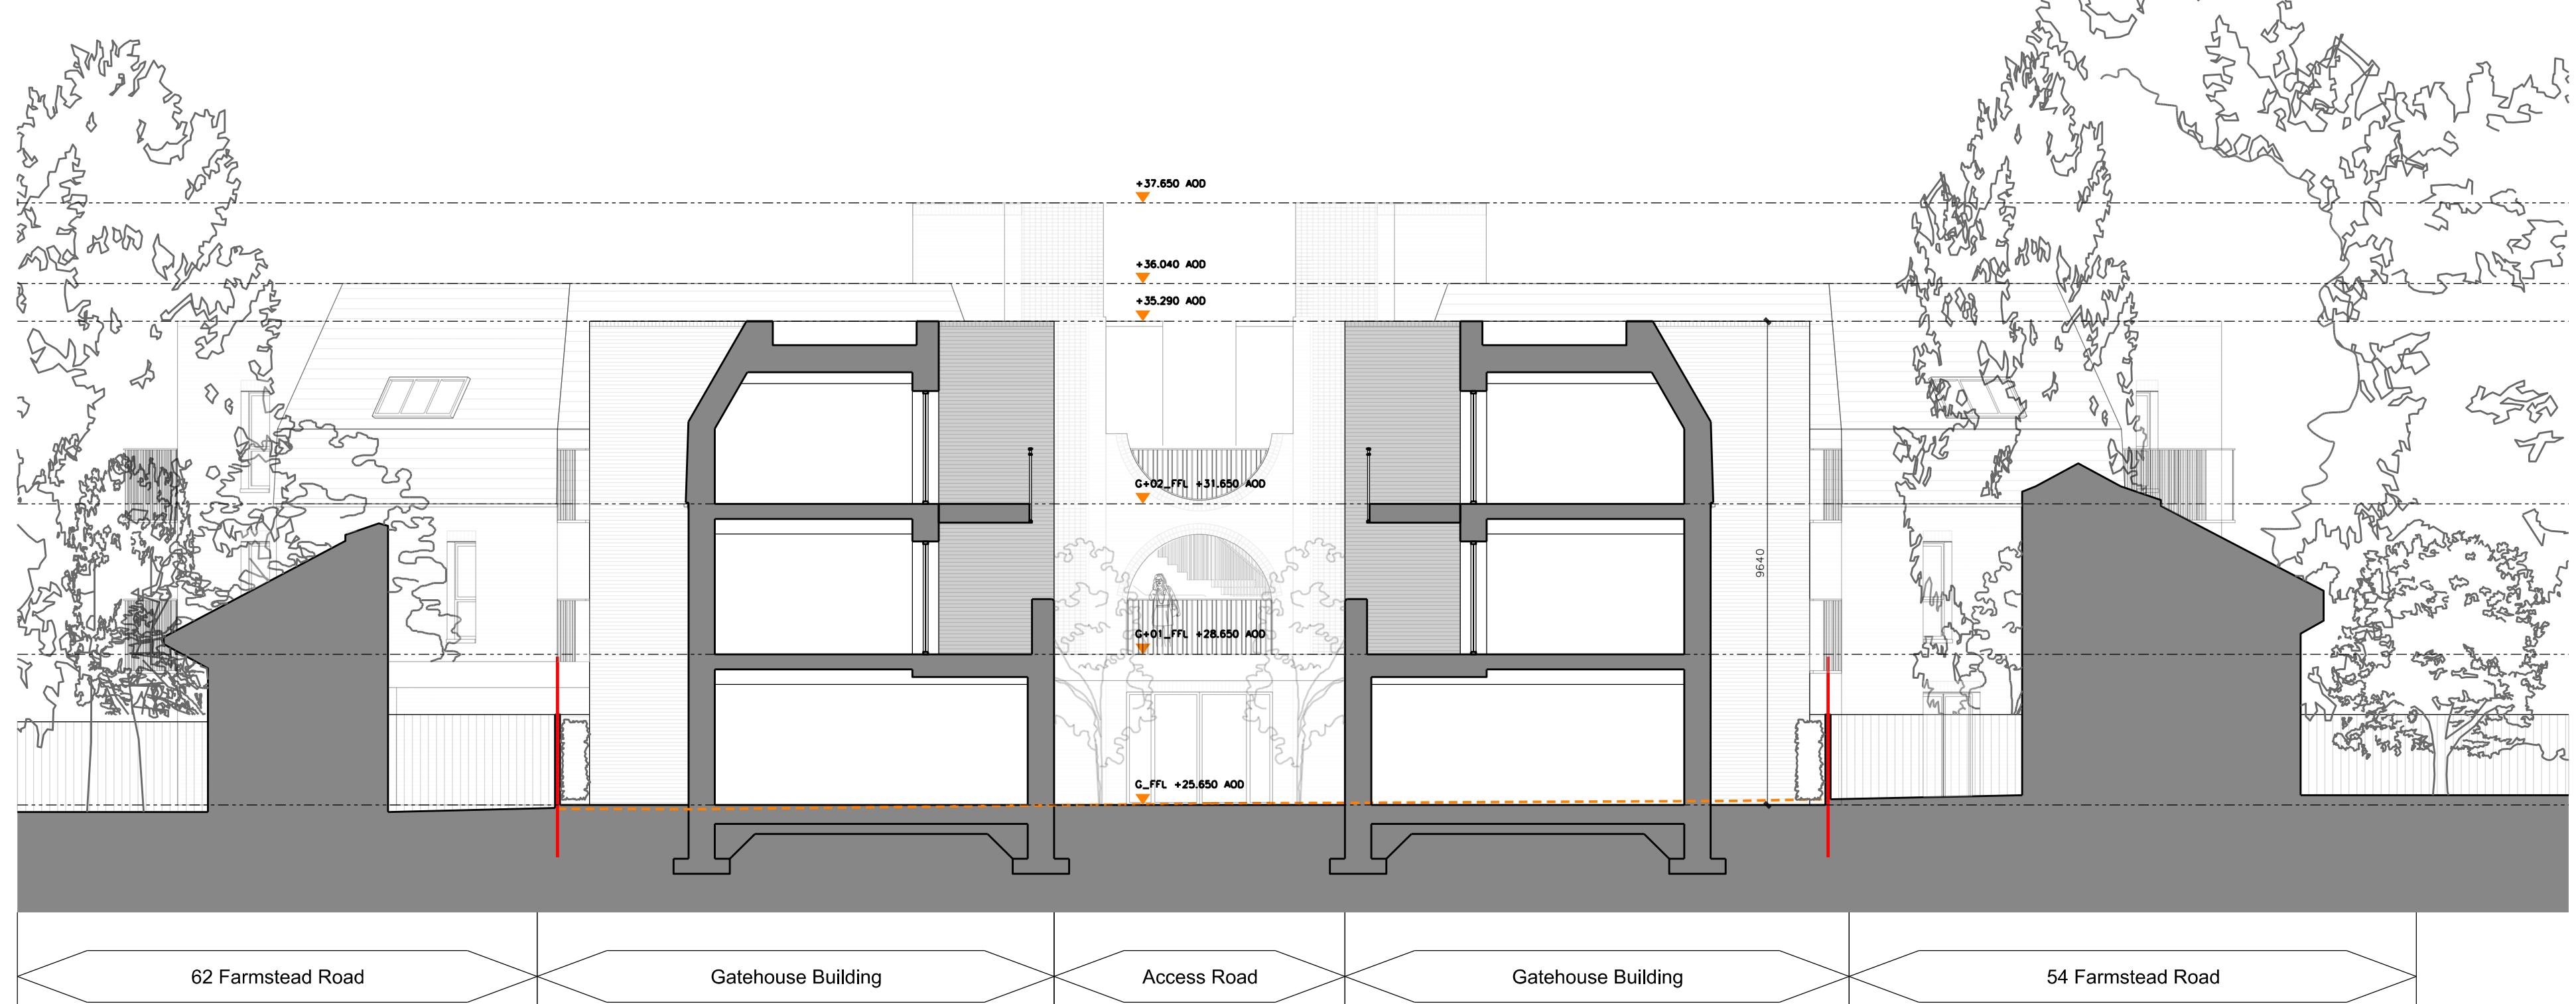


Site Section 03

Proposed Site Sections

Revision Date Description  
By Check Client Logo  
**Draft planning issue  
30/06/21**



Notes  
Do not scale drawings. All dimensions should be checked on site. Errors to be reported to architect. To be read in conjunction with all relevant architects services terms and conditions.  
Contractors, subcontractors and suppliers must verify any critical dimensions on site prior to fabrication of any building element. Any discrepancies are to be reported to the architect.  
This drawing should be read in conjunction with all relevant specifications, engineers reports and manufacturers instructions. Key dimensions must be reported prior to installation.

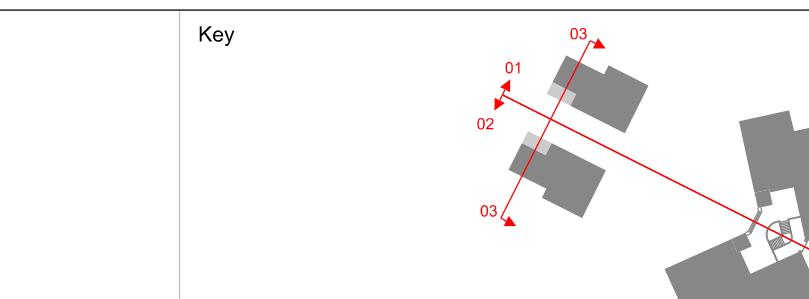

**Metropolitan Workshop**  
14-16 Cowcross Street  
London, EC1M 6DG  
+44 (0) 20 7566 0450  
www.metwork.co.uk

Project:	Farmstead Road
Client:	Phoenix Community Housing
Location:	Farmstead Road, Bellington, London, SE6 3ED
Title:	Proposed Site Sections
Date:	June 2021
Scale:	1:100 @ A0
Drawing number:	1627
Job No.	P
Status	103
Package	103
Reference	00
Revision	00